

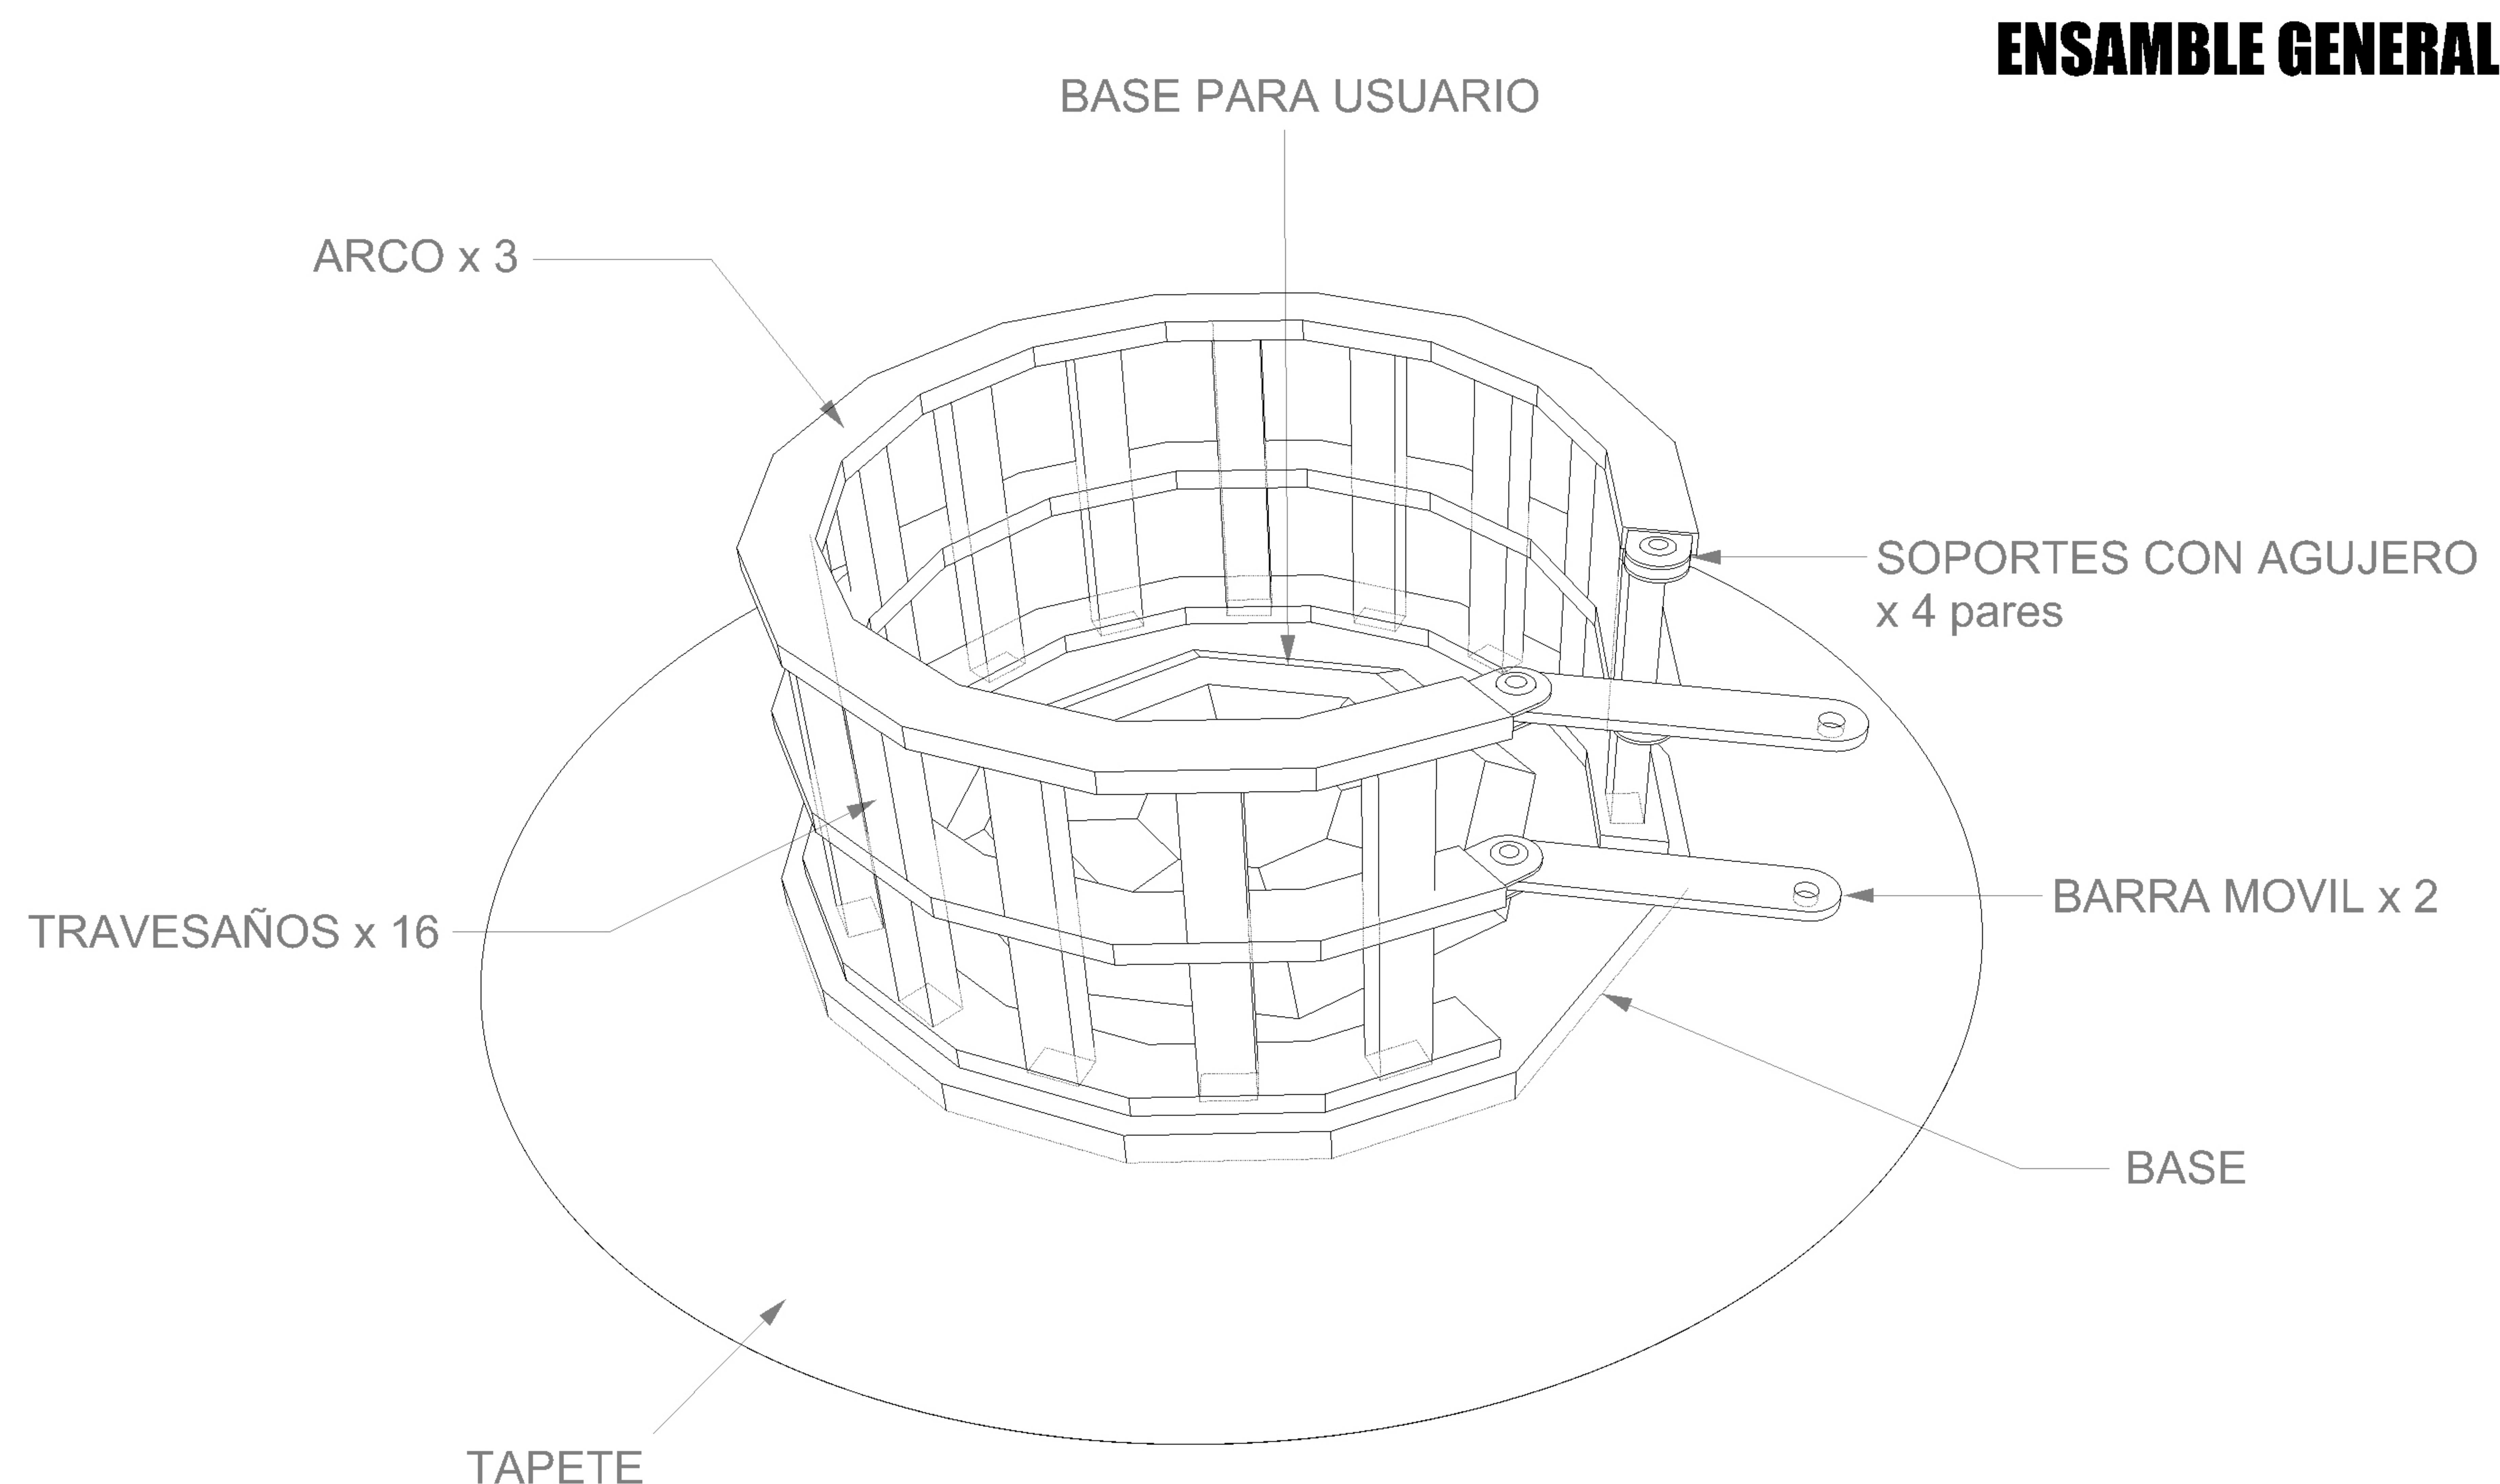


PLANO 1. Ensamble General.

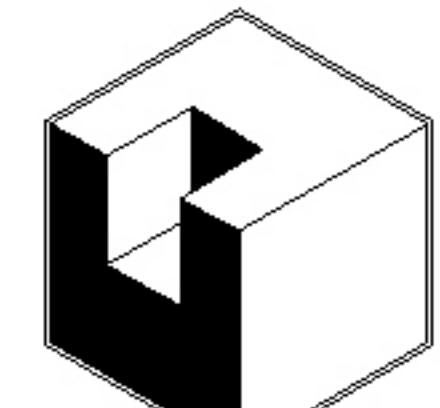

PROYECTO_Estructura caminar	DIMENSIONES GRALES: 270.00 x 120.00 x 259.72	ENSAMBLE GENERAL	11.MAYO.2020	
Estructura	OBSERVACIONES:		ACT. CM	
DIBUJO: fiscortes STUDIO	MATERIALES: ESTRUCTURA DE MDF // TRIPLEY DE 16MM CON LAMINADO PLÁSTICO O ACABADOS SEGÚN CLIENTE		ESC. -	
			HOJA -	


PLANO 2. Vista Explosiva.

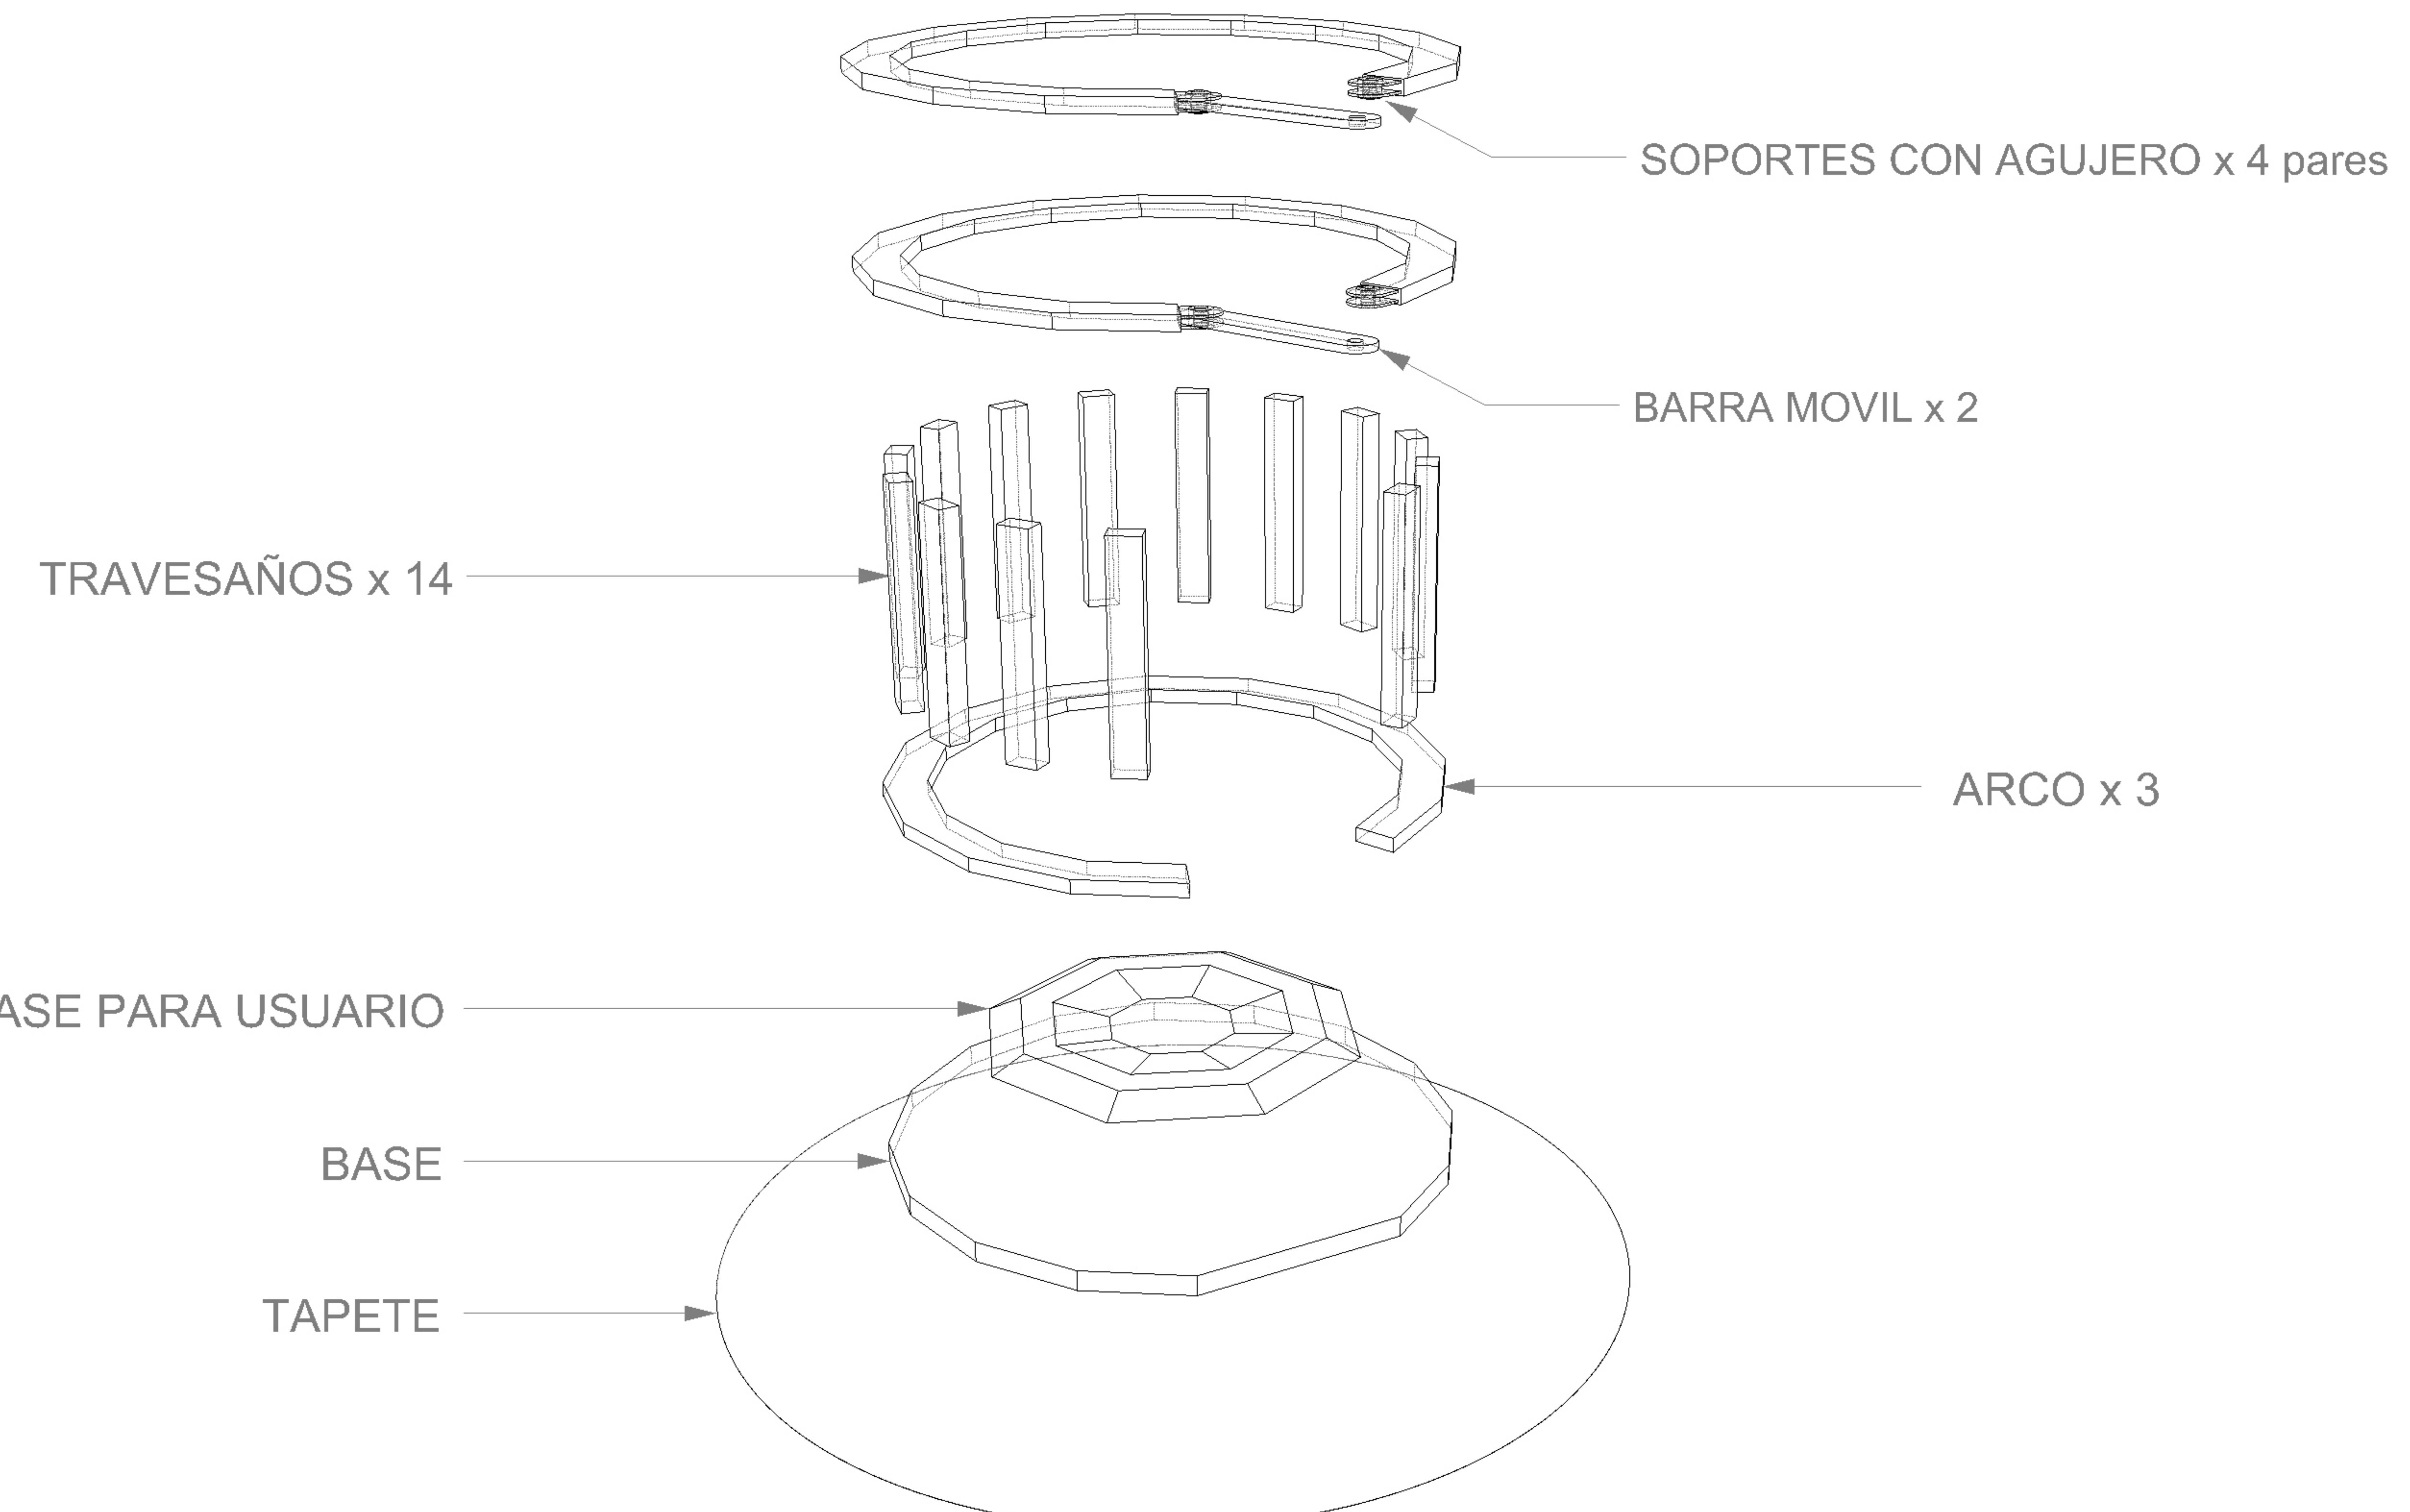


PROYECTO_Estructura caminar	DIMENSIONES GRALES: 270.00 x 120.00 x 259.72	ENSAMBLE GENERAL	11.MAYO.2020	C
Estructura	OBSERVACIONES: MATERIALES: ESTRUCTURA DE MDF // TRIPLAY DE 16MM CON LAMINADO PLÁSTICO O ACABADOS SEGÚN CLIENTE		ACT. CM	
DIBUJÓ: fiscortes STUDIO			ESC. -	
			HOJA -	

PLANO 3. Vistas Ensamble General


VISTA SUPERIOR

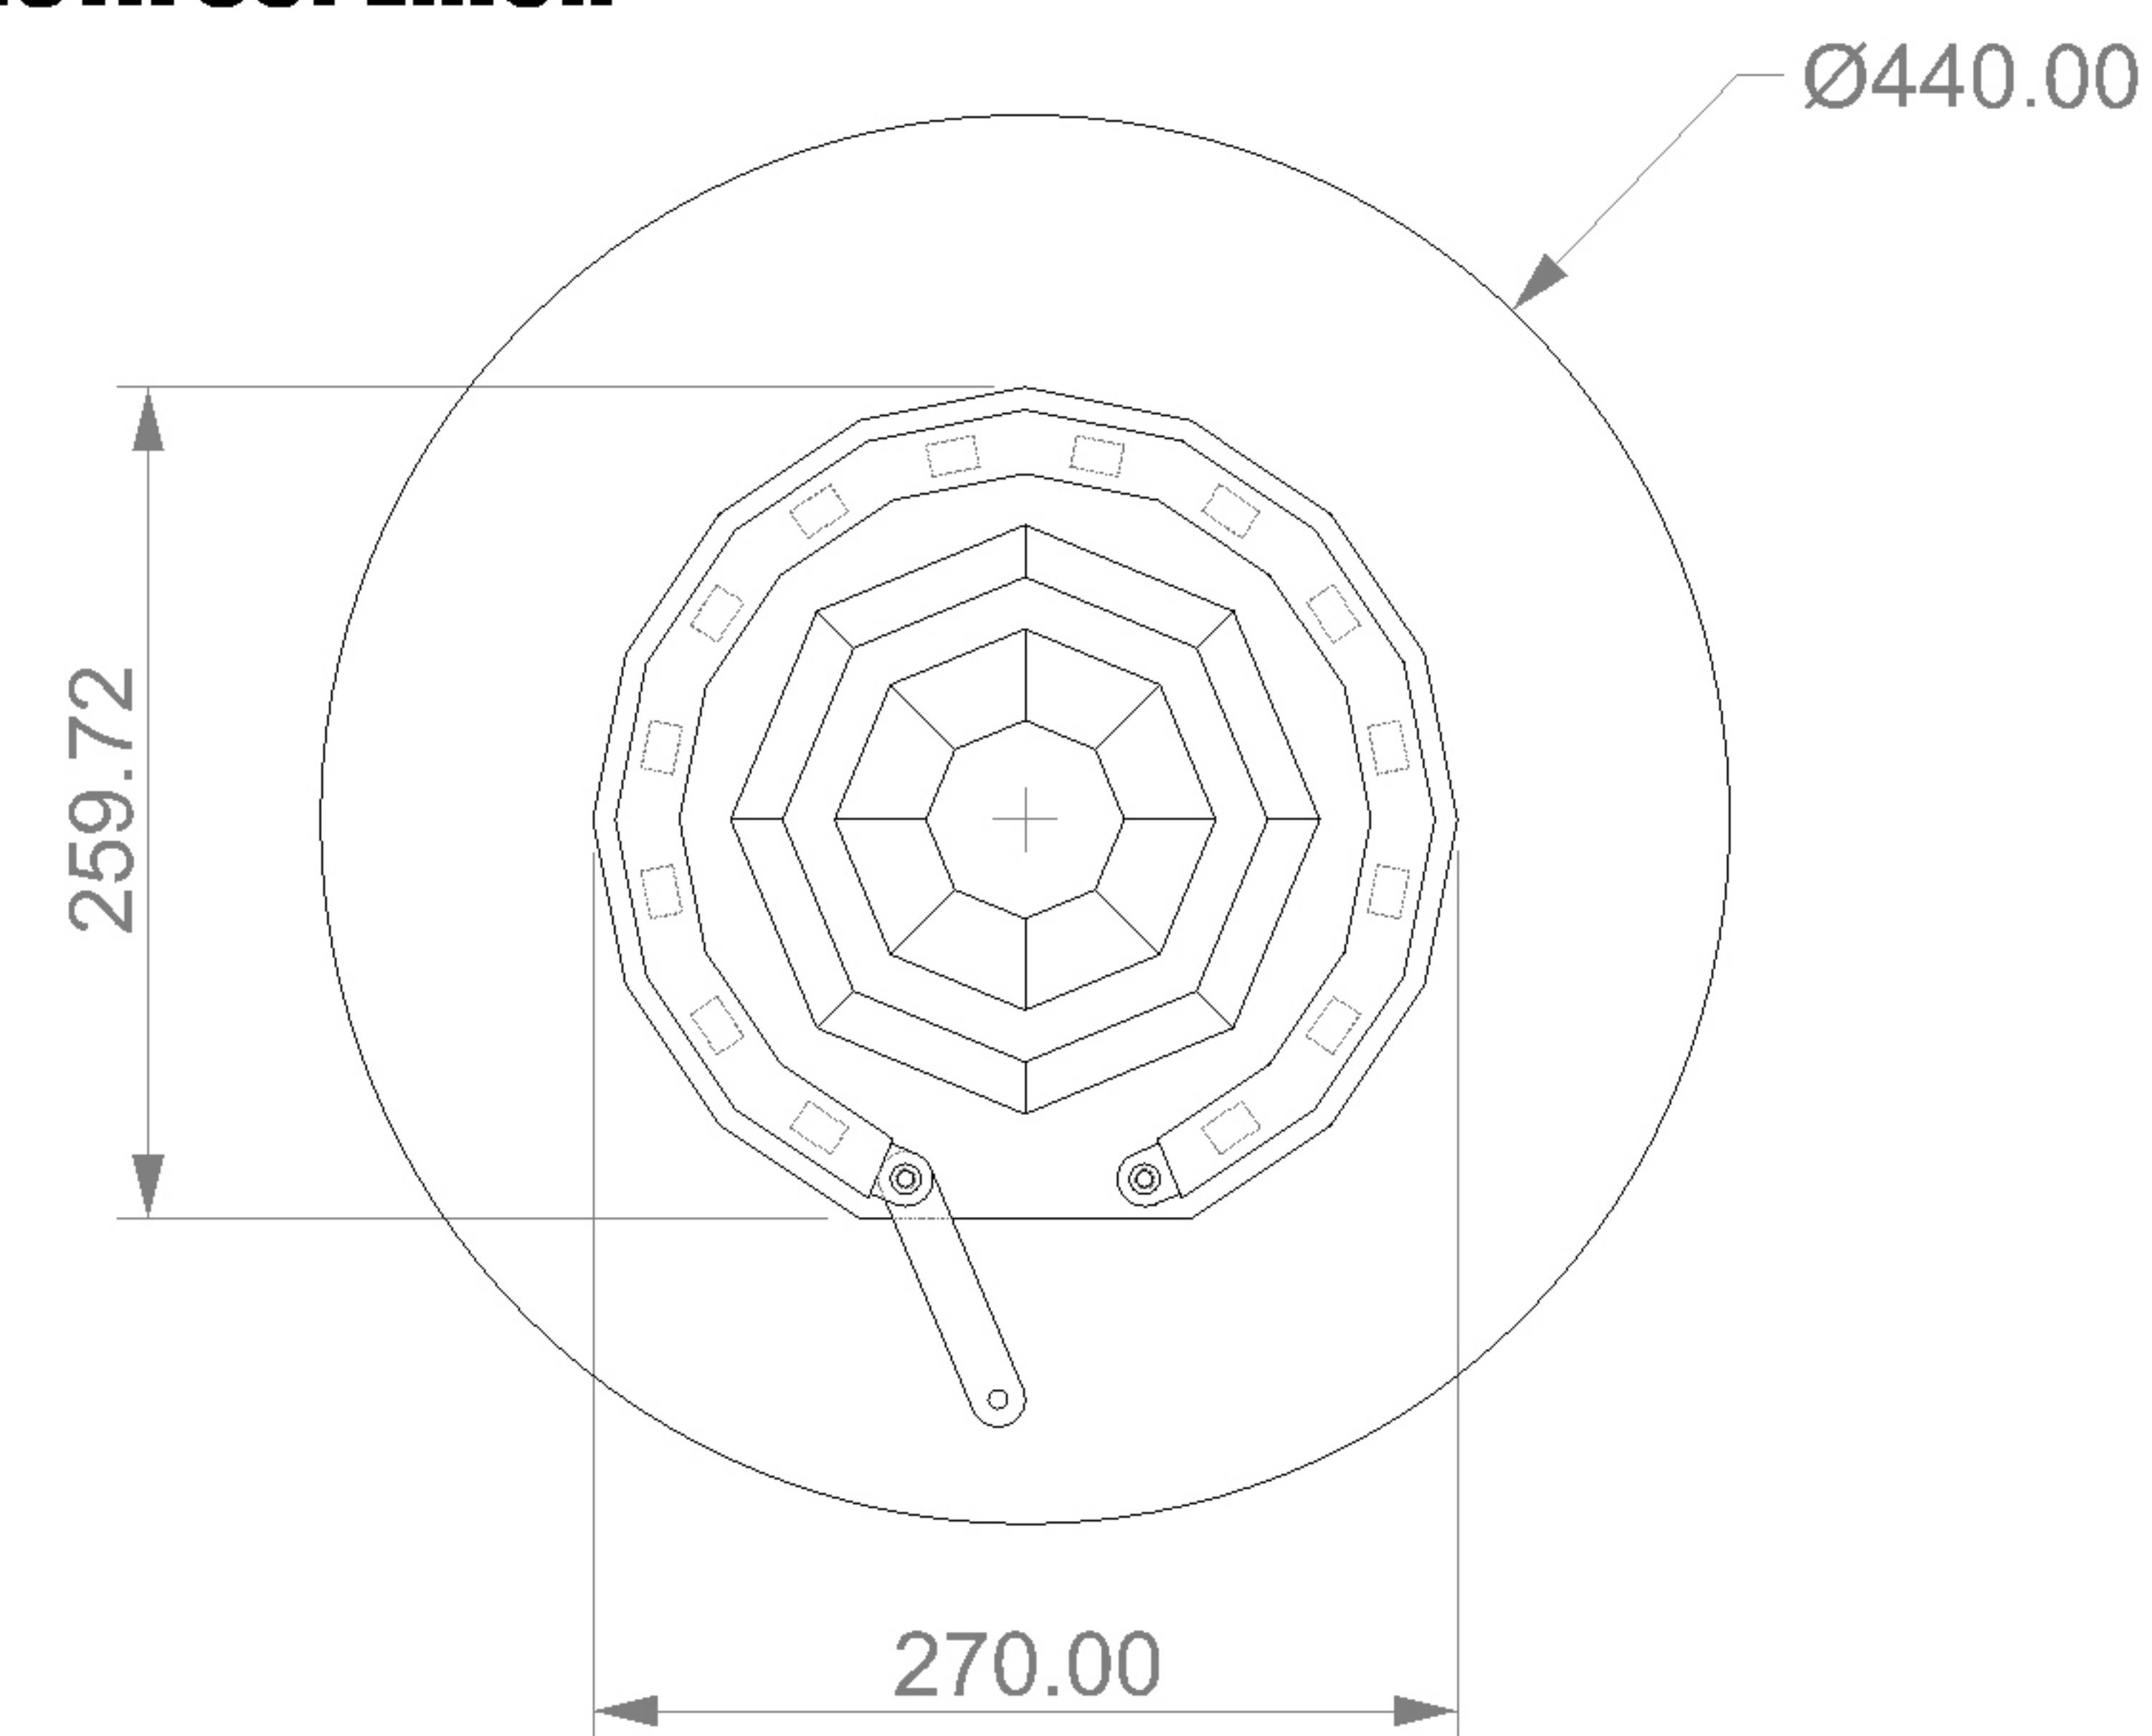


VISTA PERSPECTIVA

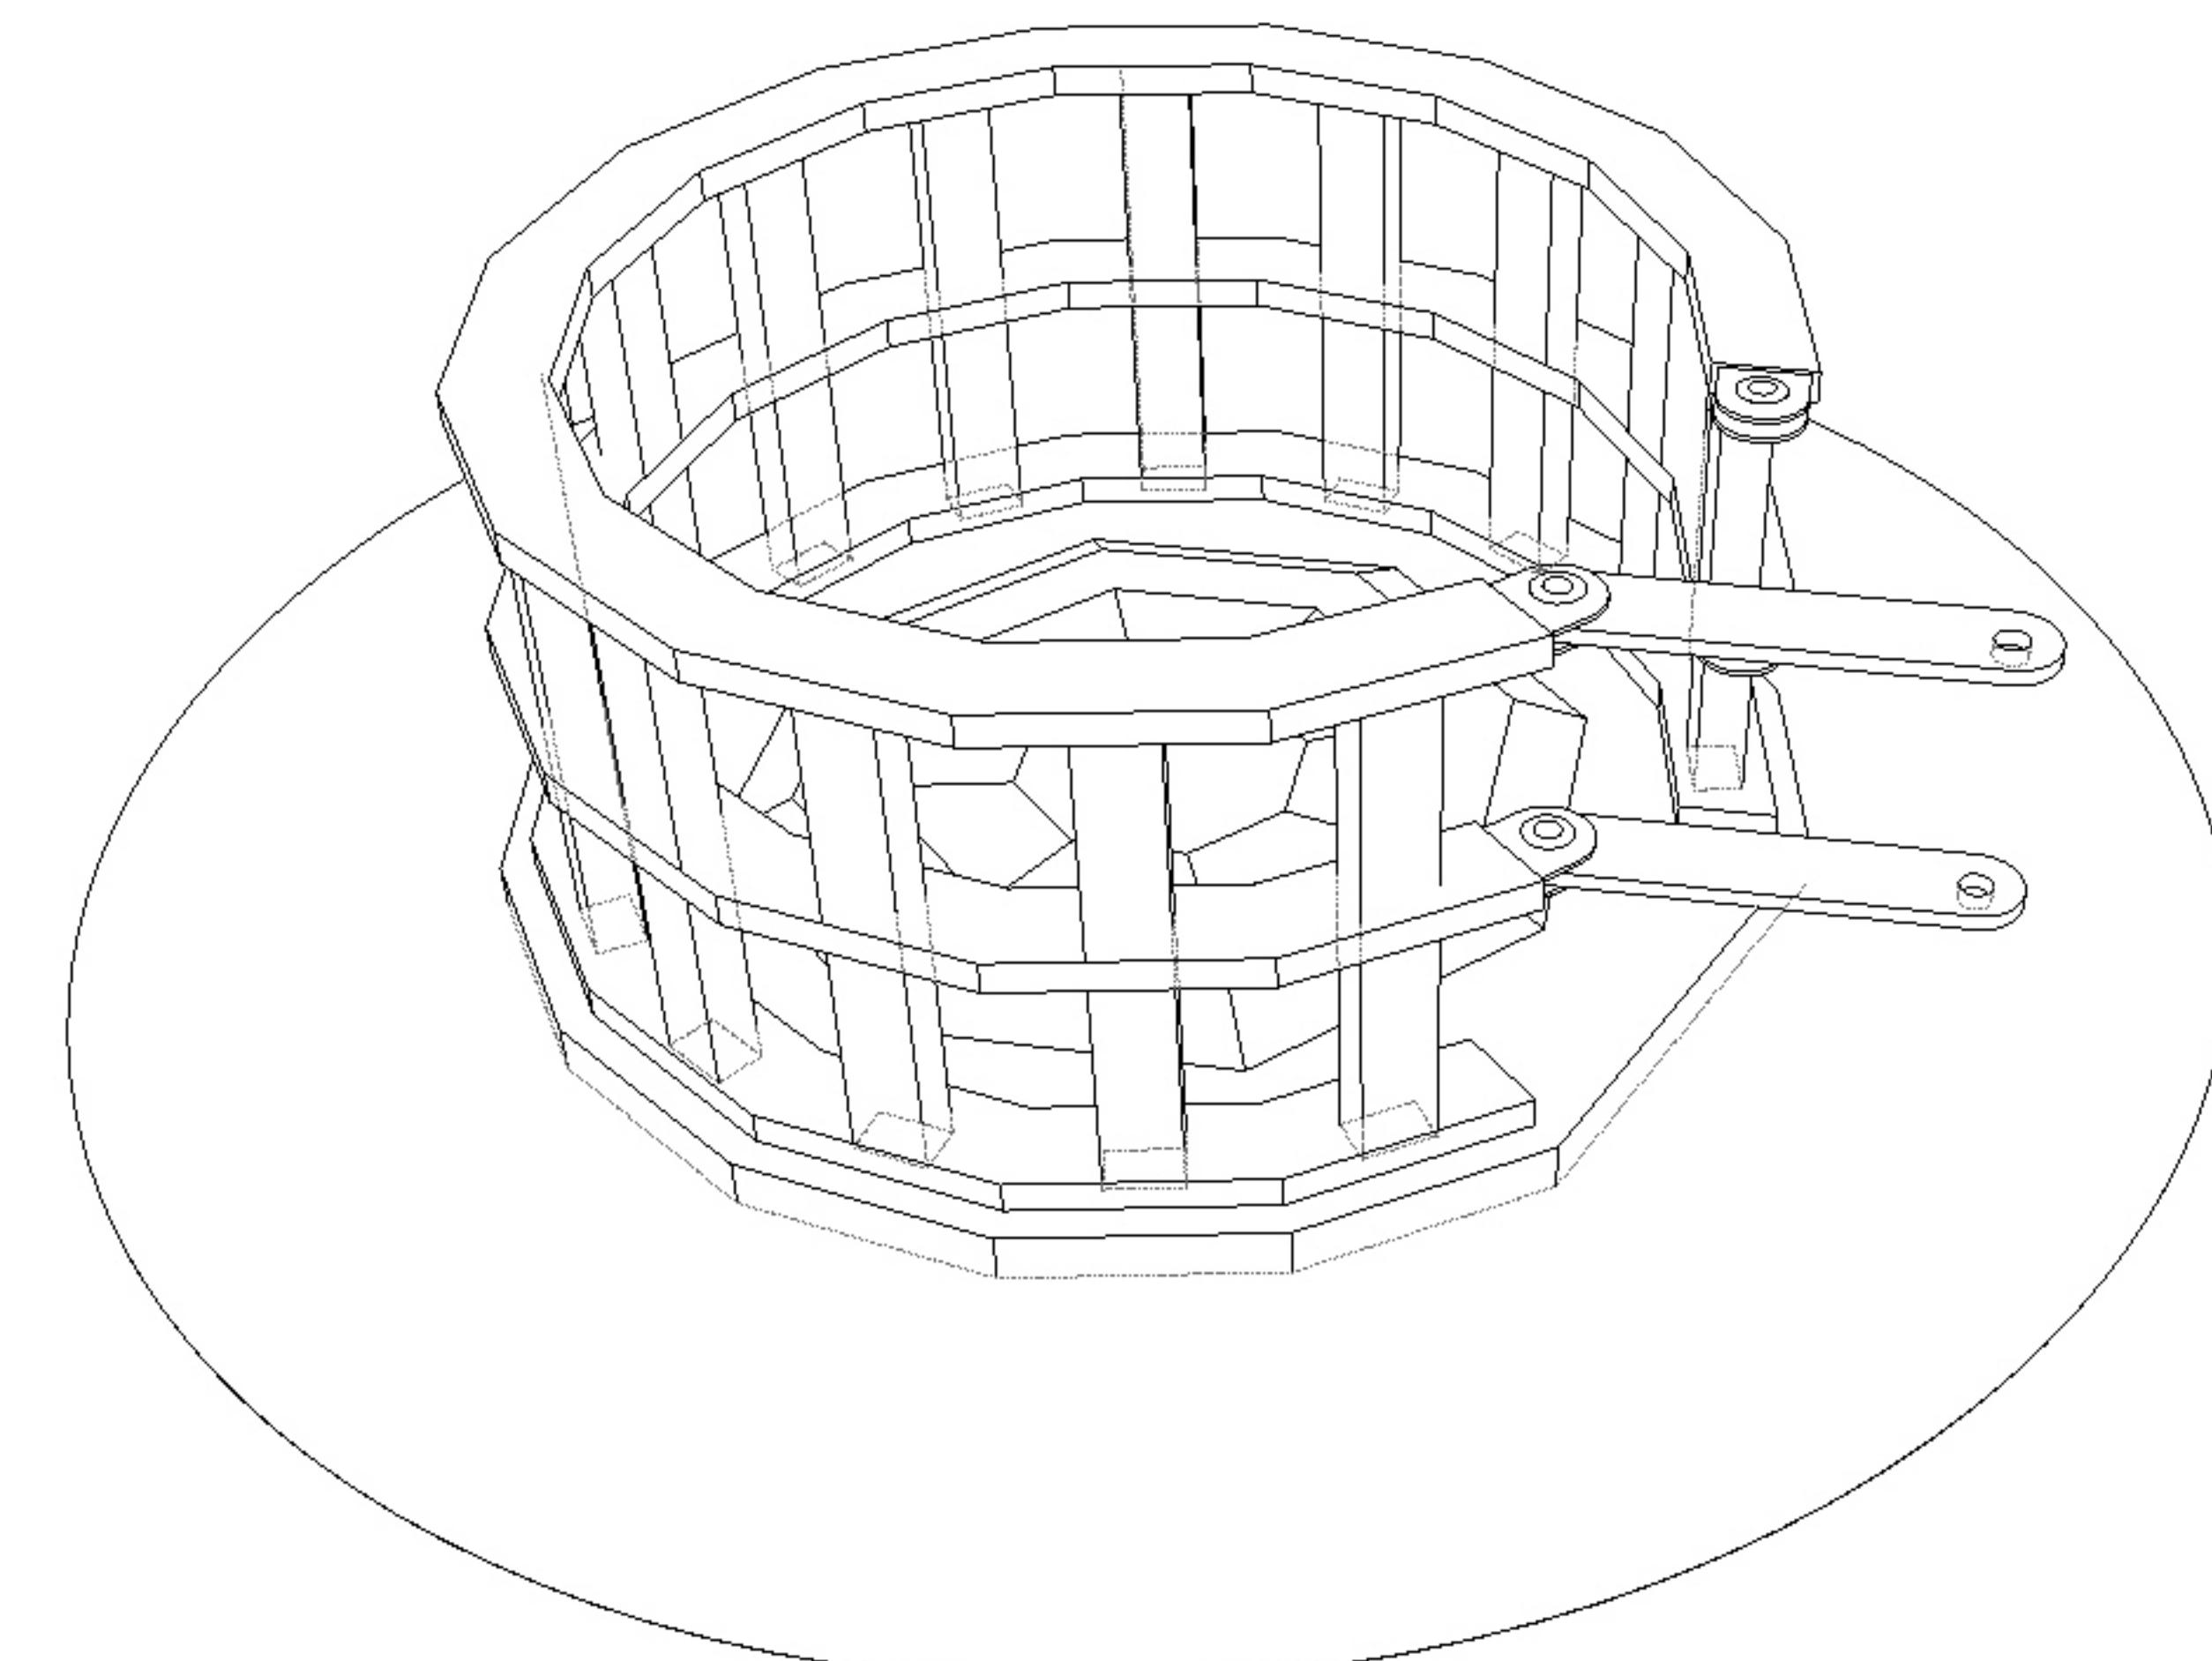

VISTA FRONTAL

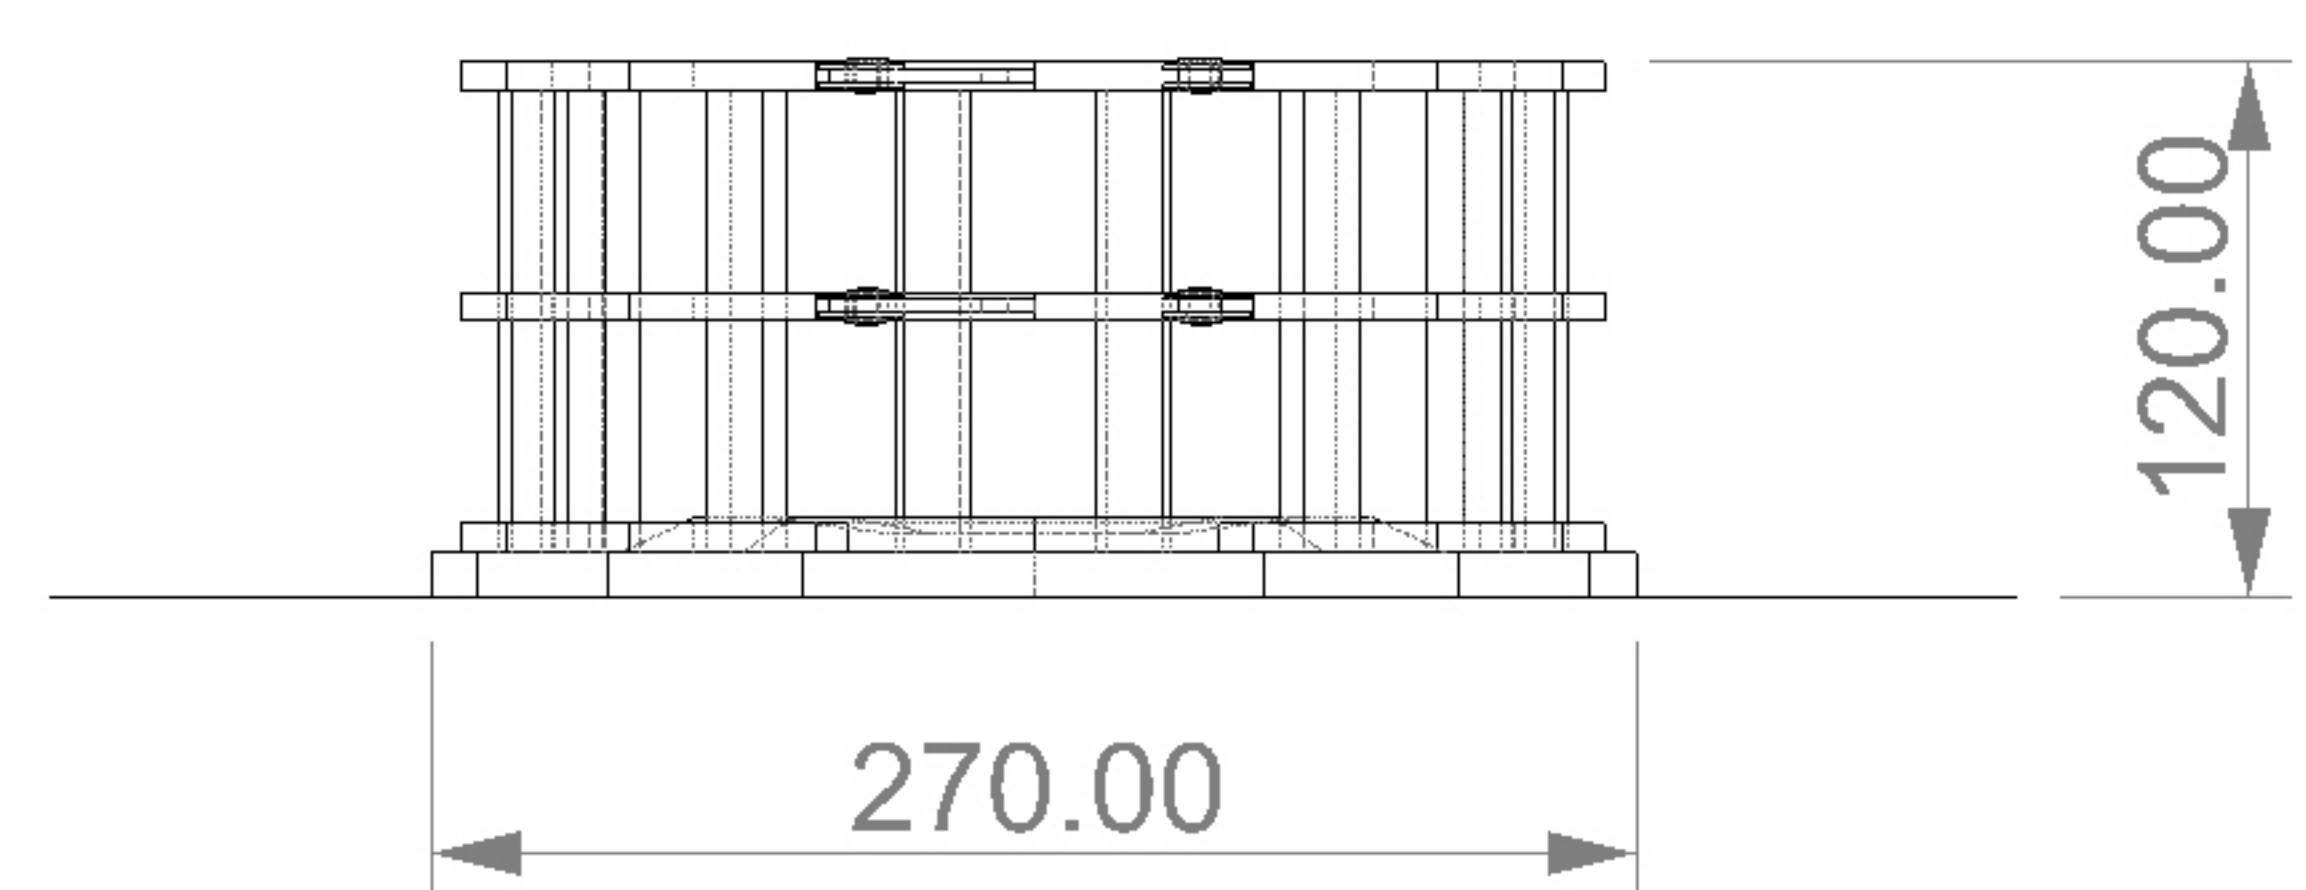


VISTA LATERAL

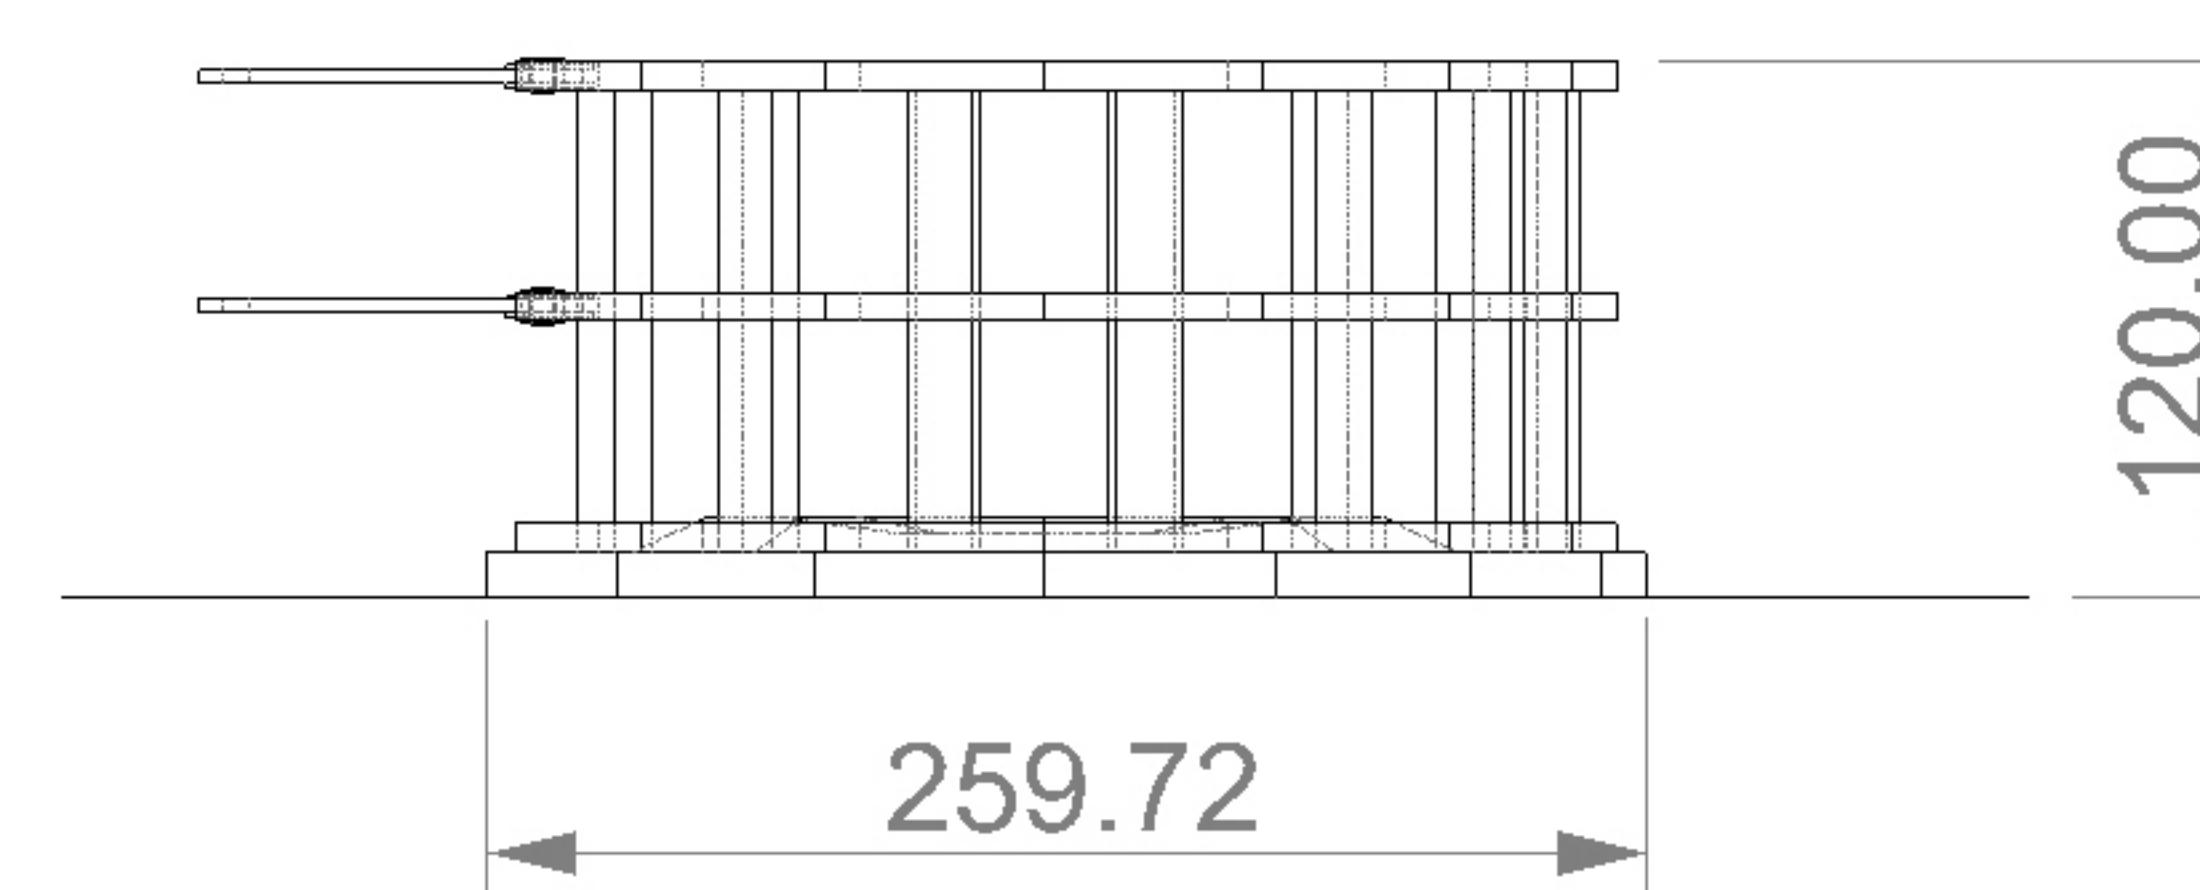


PROYECTO_Estructura caminar	DIMENSIONES GRALES: 270.00 x 120.00 x 259.72	ENSAMBLE GENERAL	11.MAYO.2020	
Estructura	OBSERVACIONES:		ACT. CM	
DIBUJÓ:fiscortes STUDIO	MATERIALES: ESTRUCTURA DE MDF // TRIPLEY DE 16MM CON LAMINADO PLÁSTICO O ACABADOS SEGÚN CLIENTE		ESC. -	
			HOJA -	

PLANO 4. Arcos (x3)


VISTA SUPERIOR

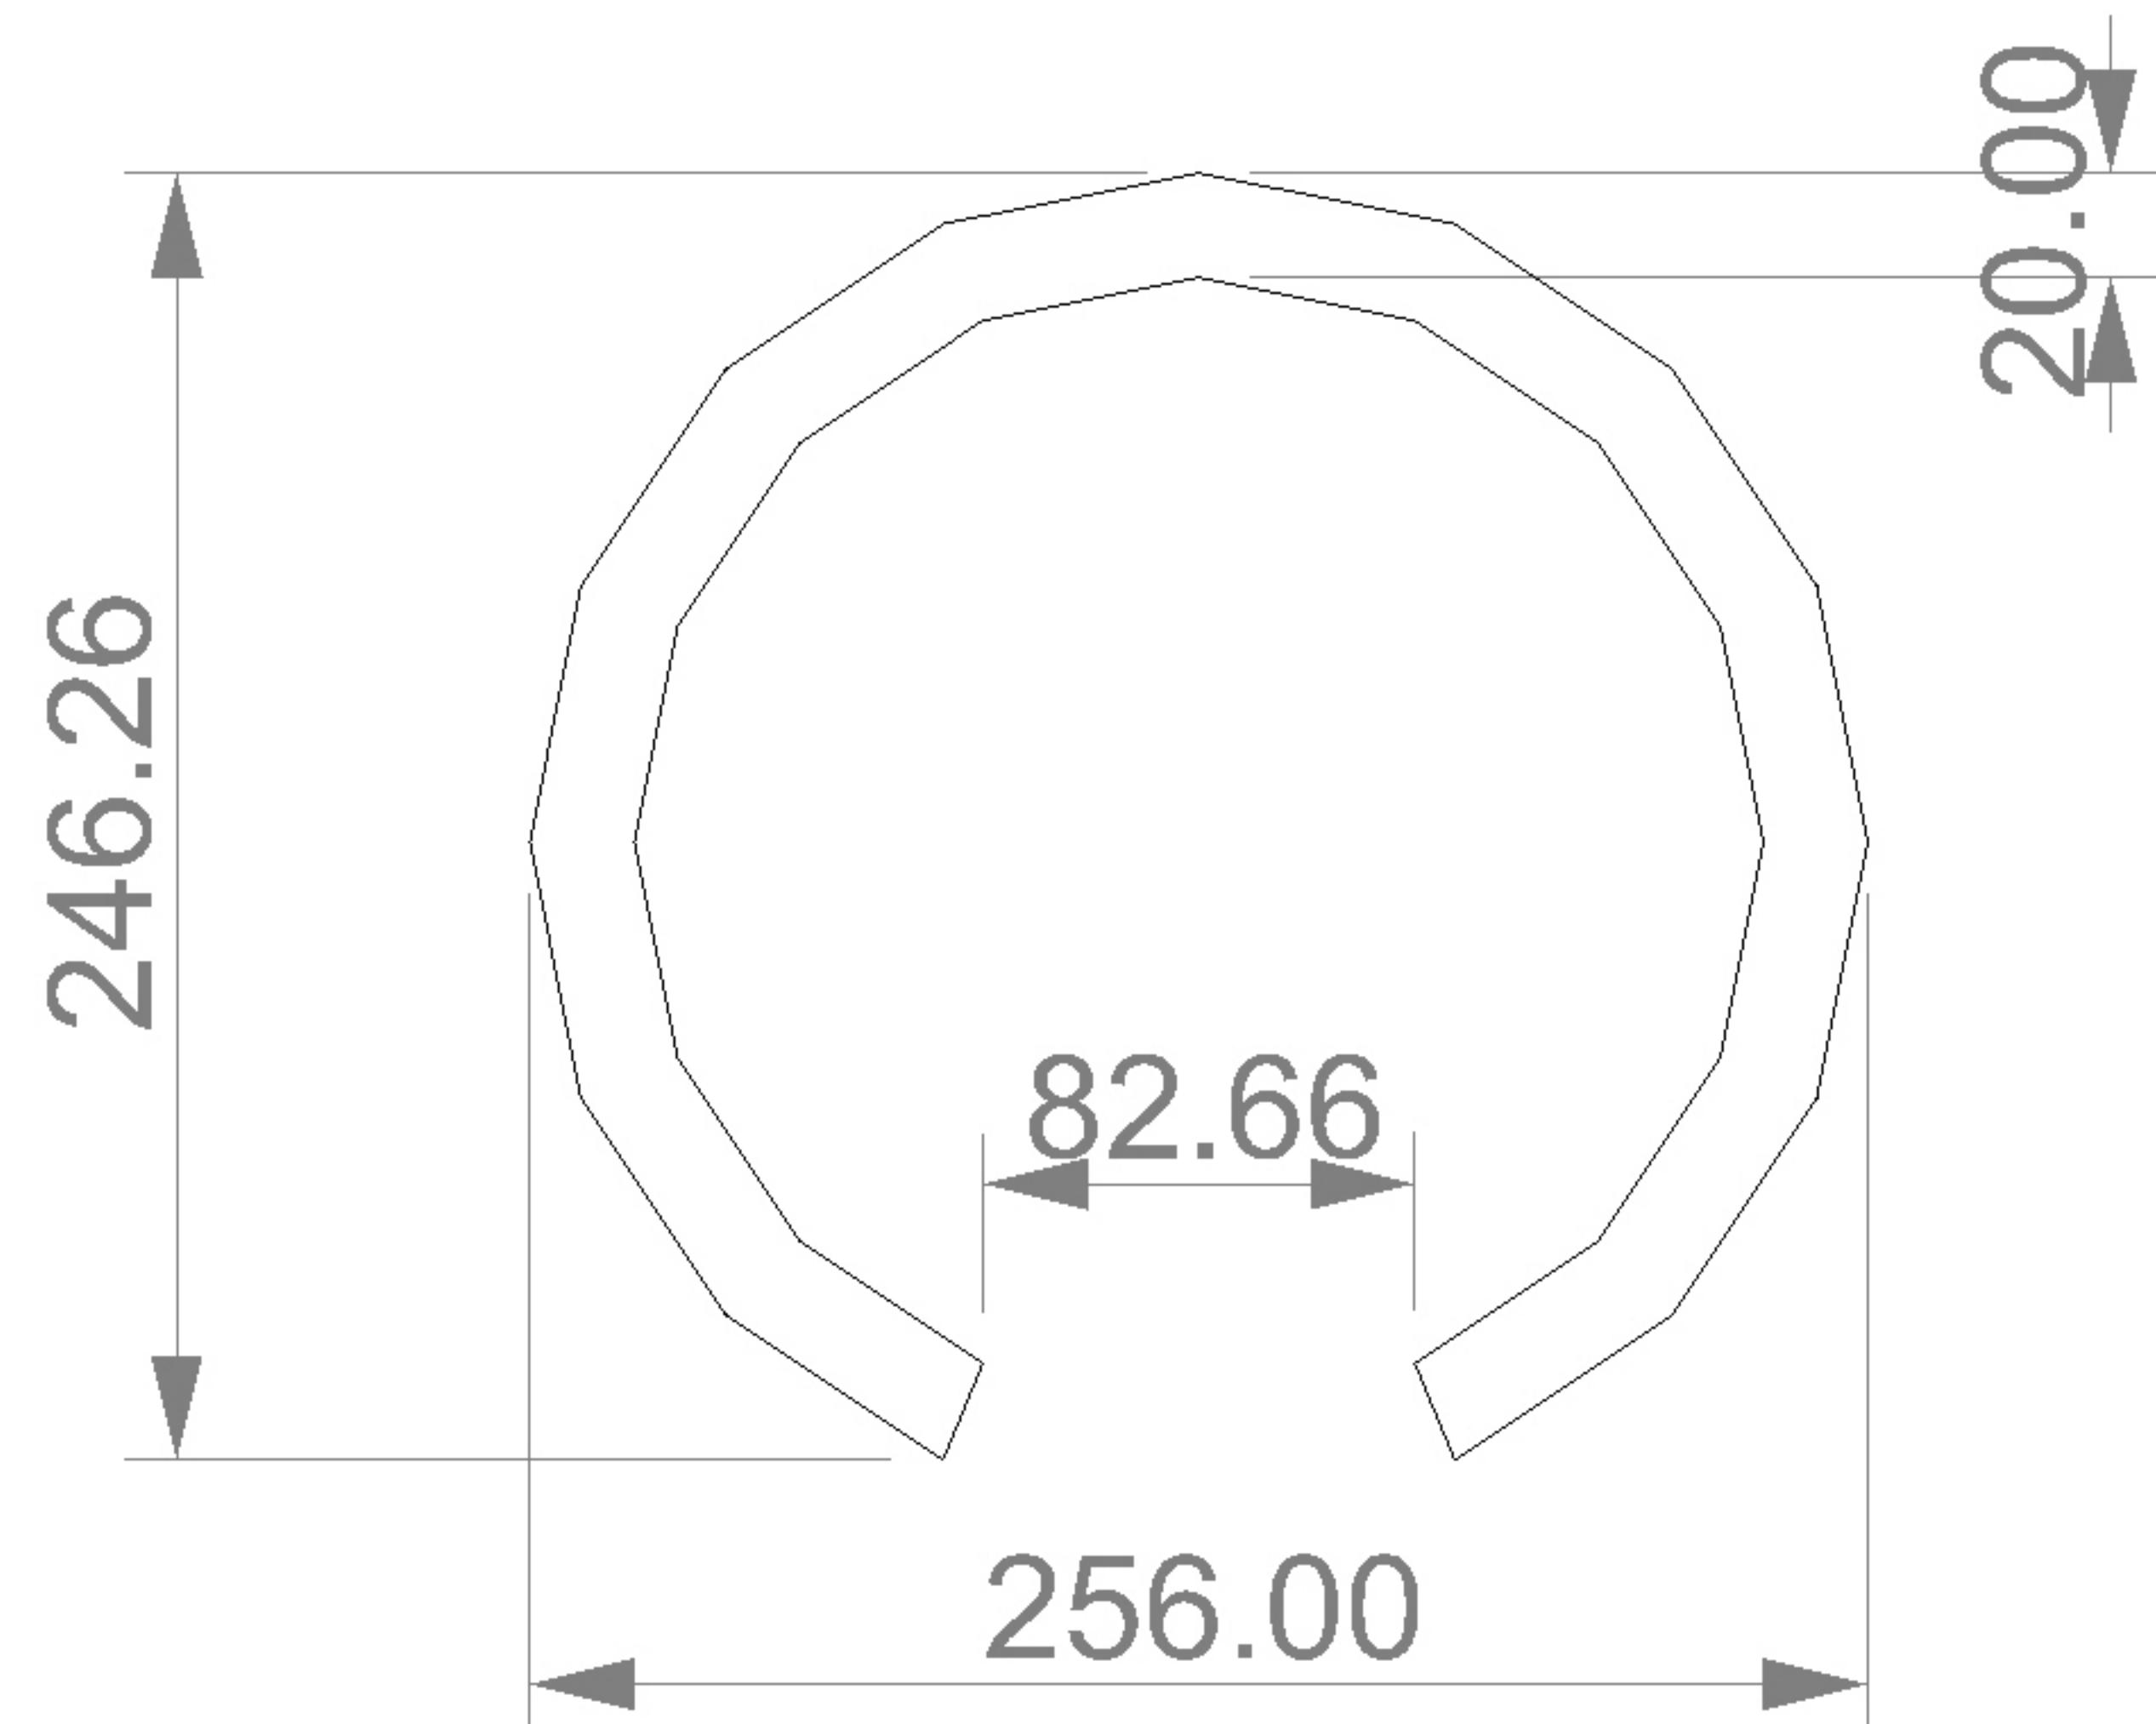


VISTA PERSPECTIVA

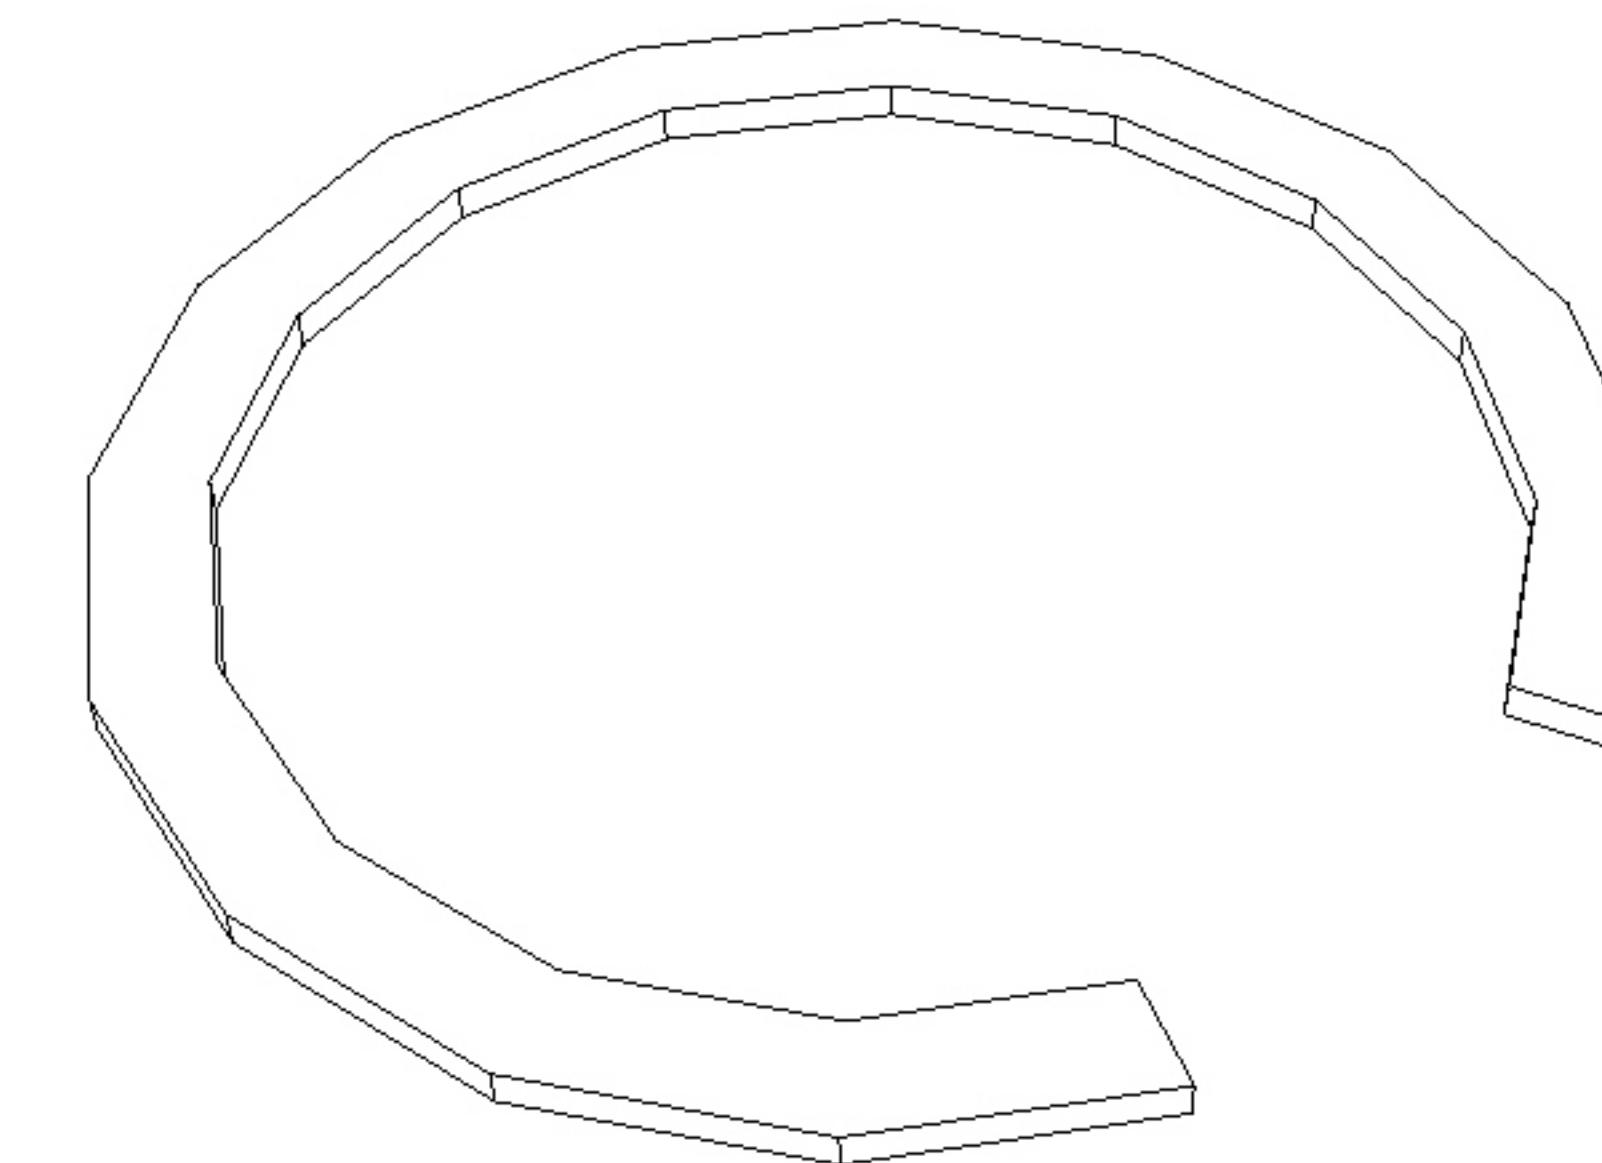

VISTA FRONTAL

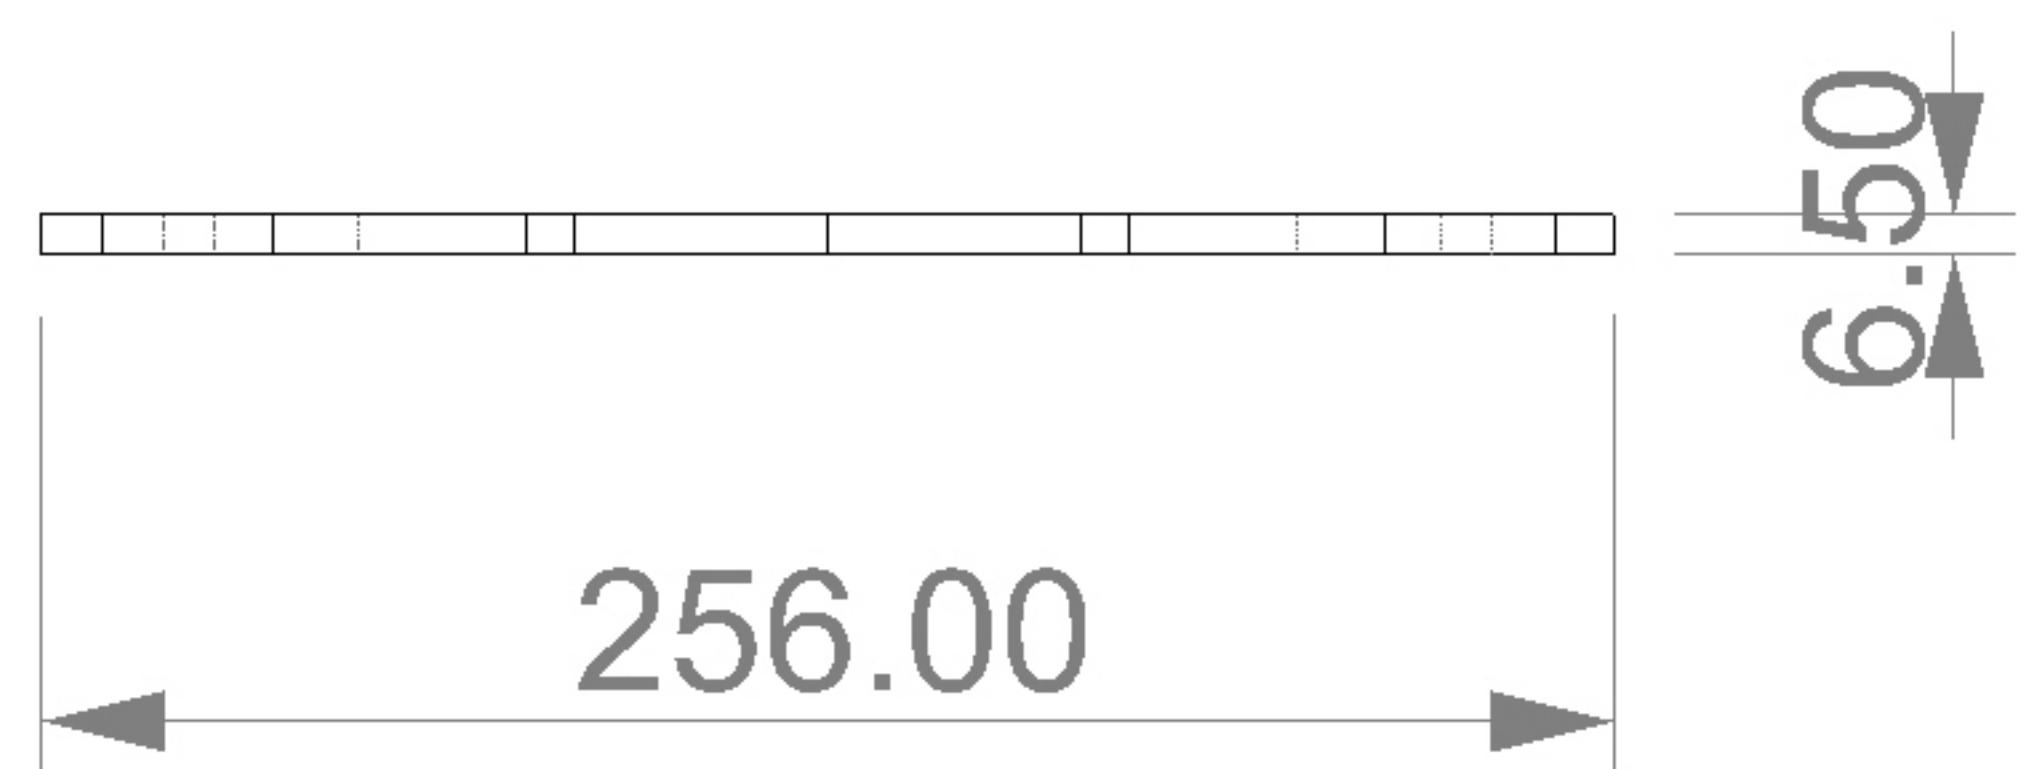


VISTA LATERAL

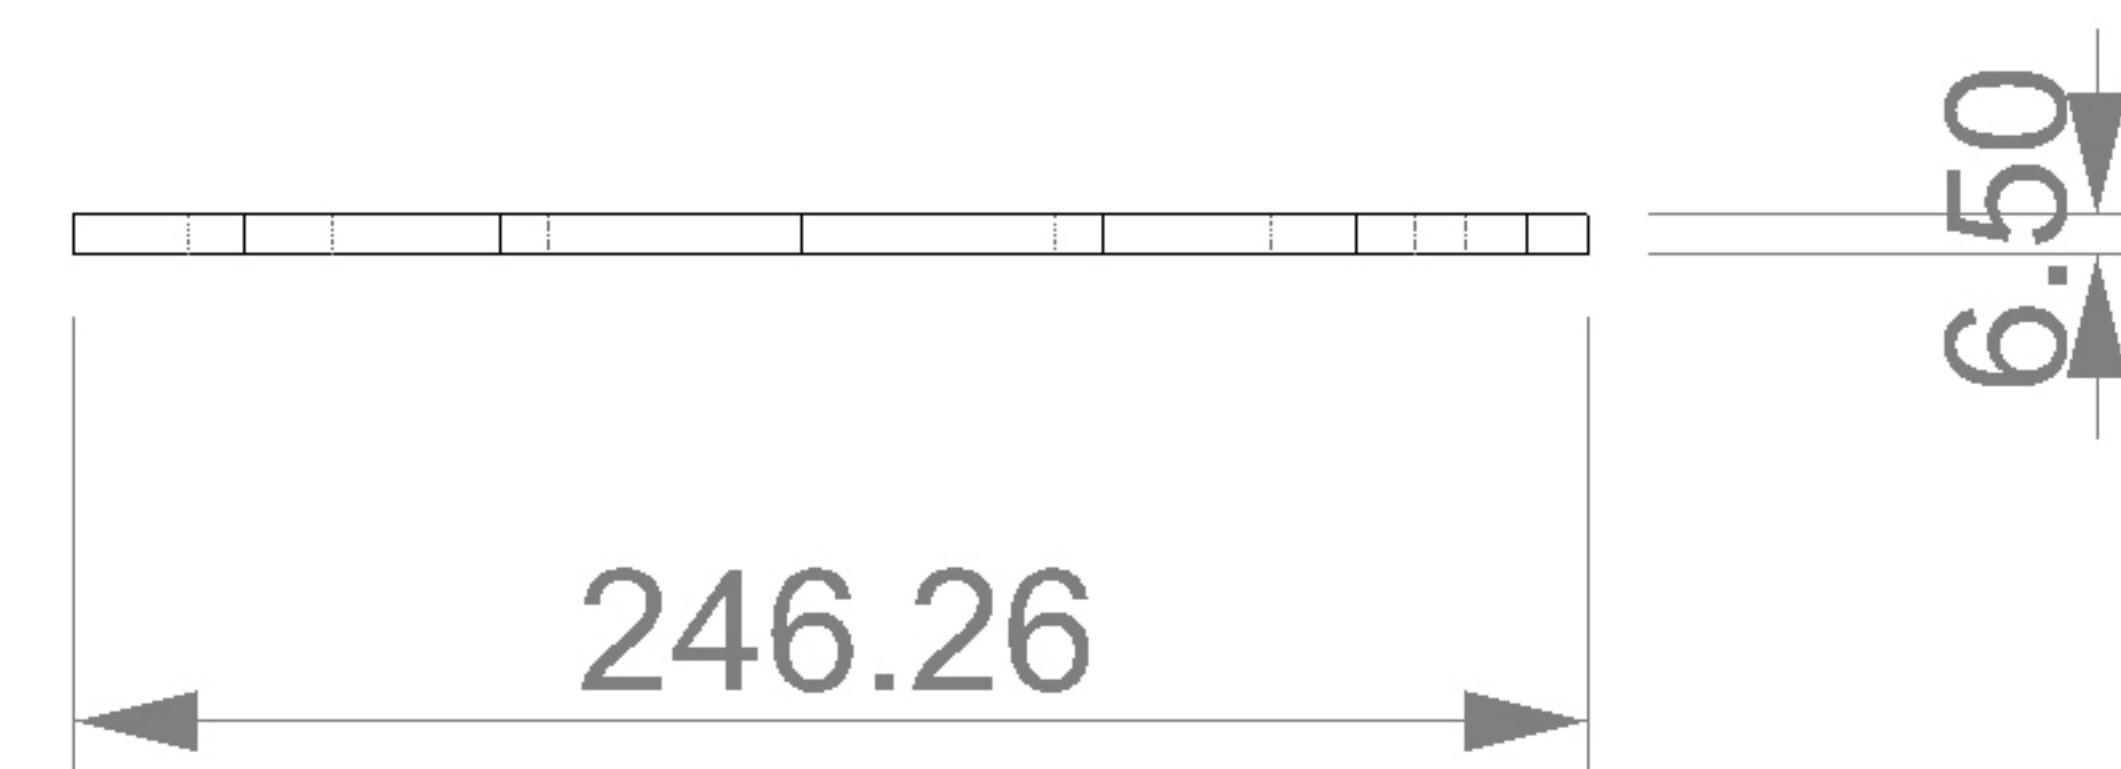

PROYECTO_Estructura caminar	DIMENSIONES GRALES: 256.00 x 6.50 x 246.26	ENSAMBLE GENERAL	11.MAYO.2020	
Estructura	OBSERVACIONES:		ACT. CM	
DIBUJÓ:fiscortes STUDIO	MATERIALES: ESTRUCTURA DE MDF // TRIPLEY DE 16MM CON LAMINADO PLÁSTICO O ACABADOS SEGÚN CLIENTE		ESC. -	
			HOJA -	





PLANO 5. Ensamble Arcos - Barras móviles.

VISTA PERSPECTIVA

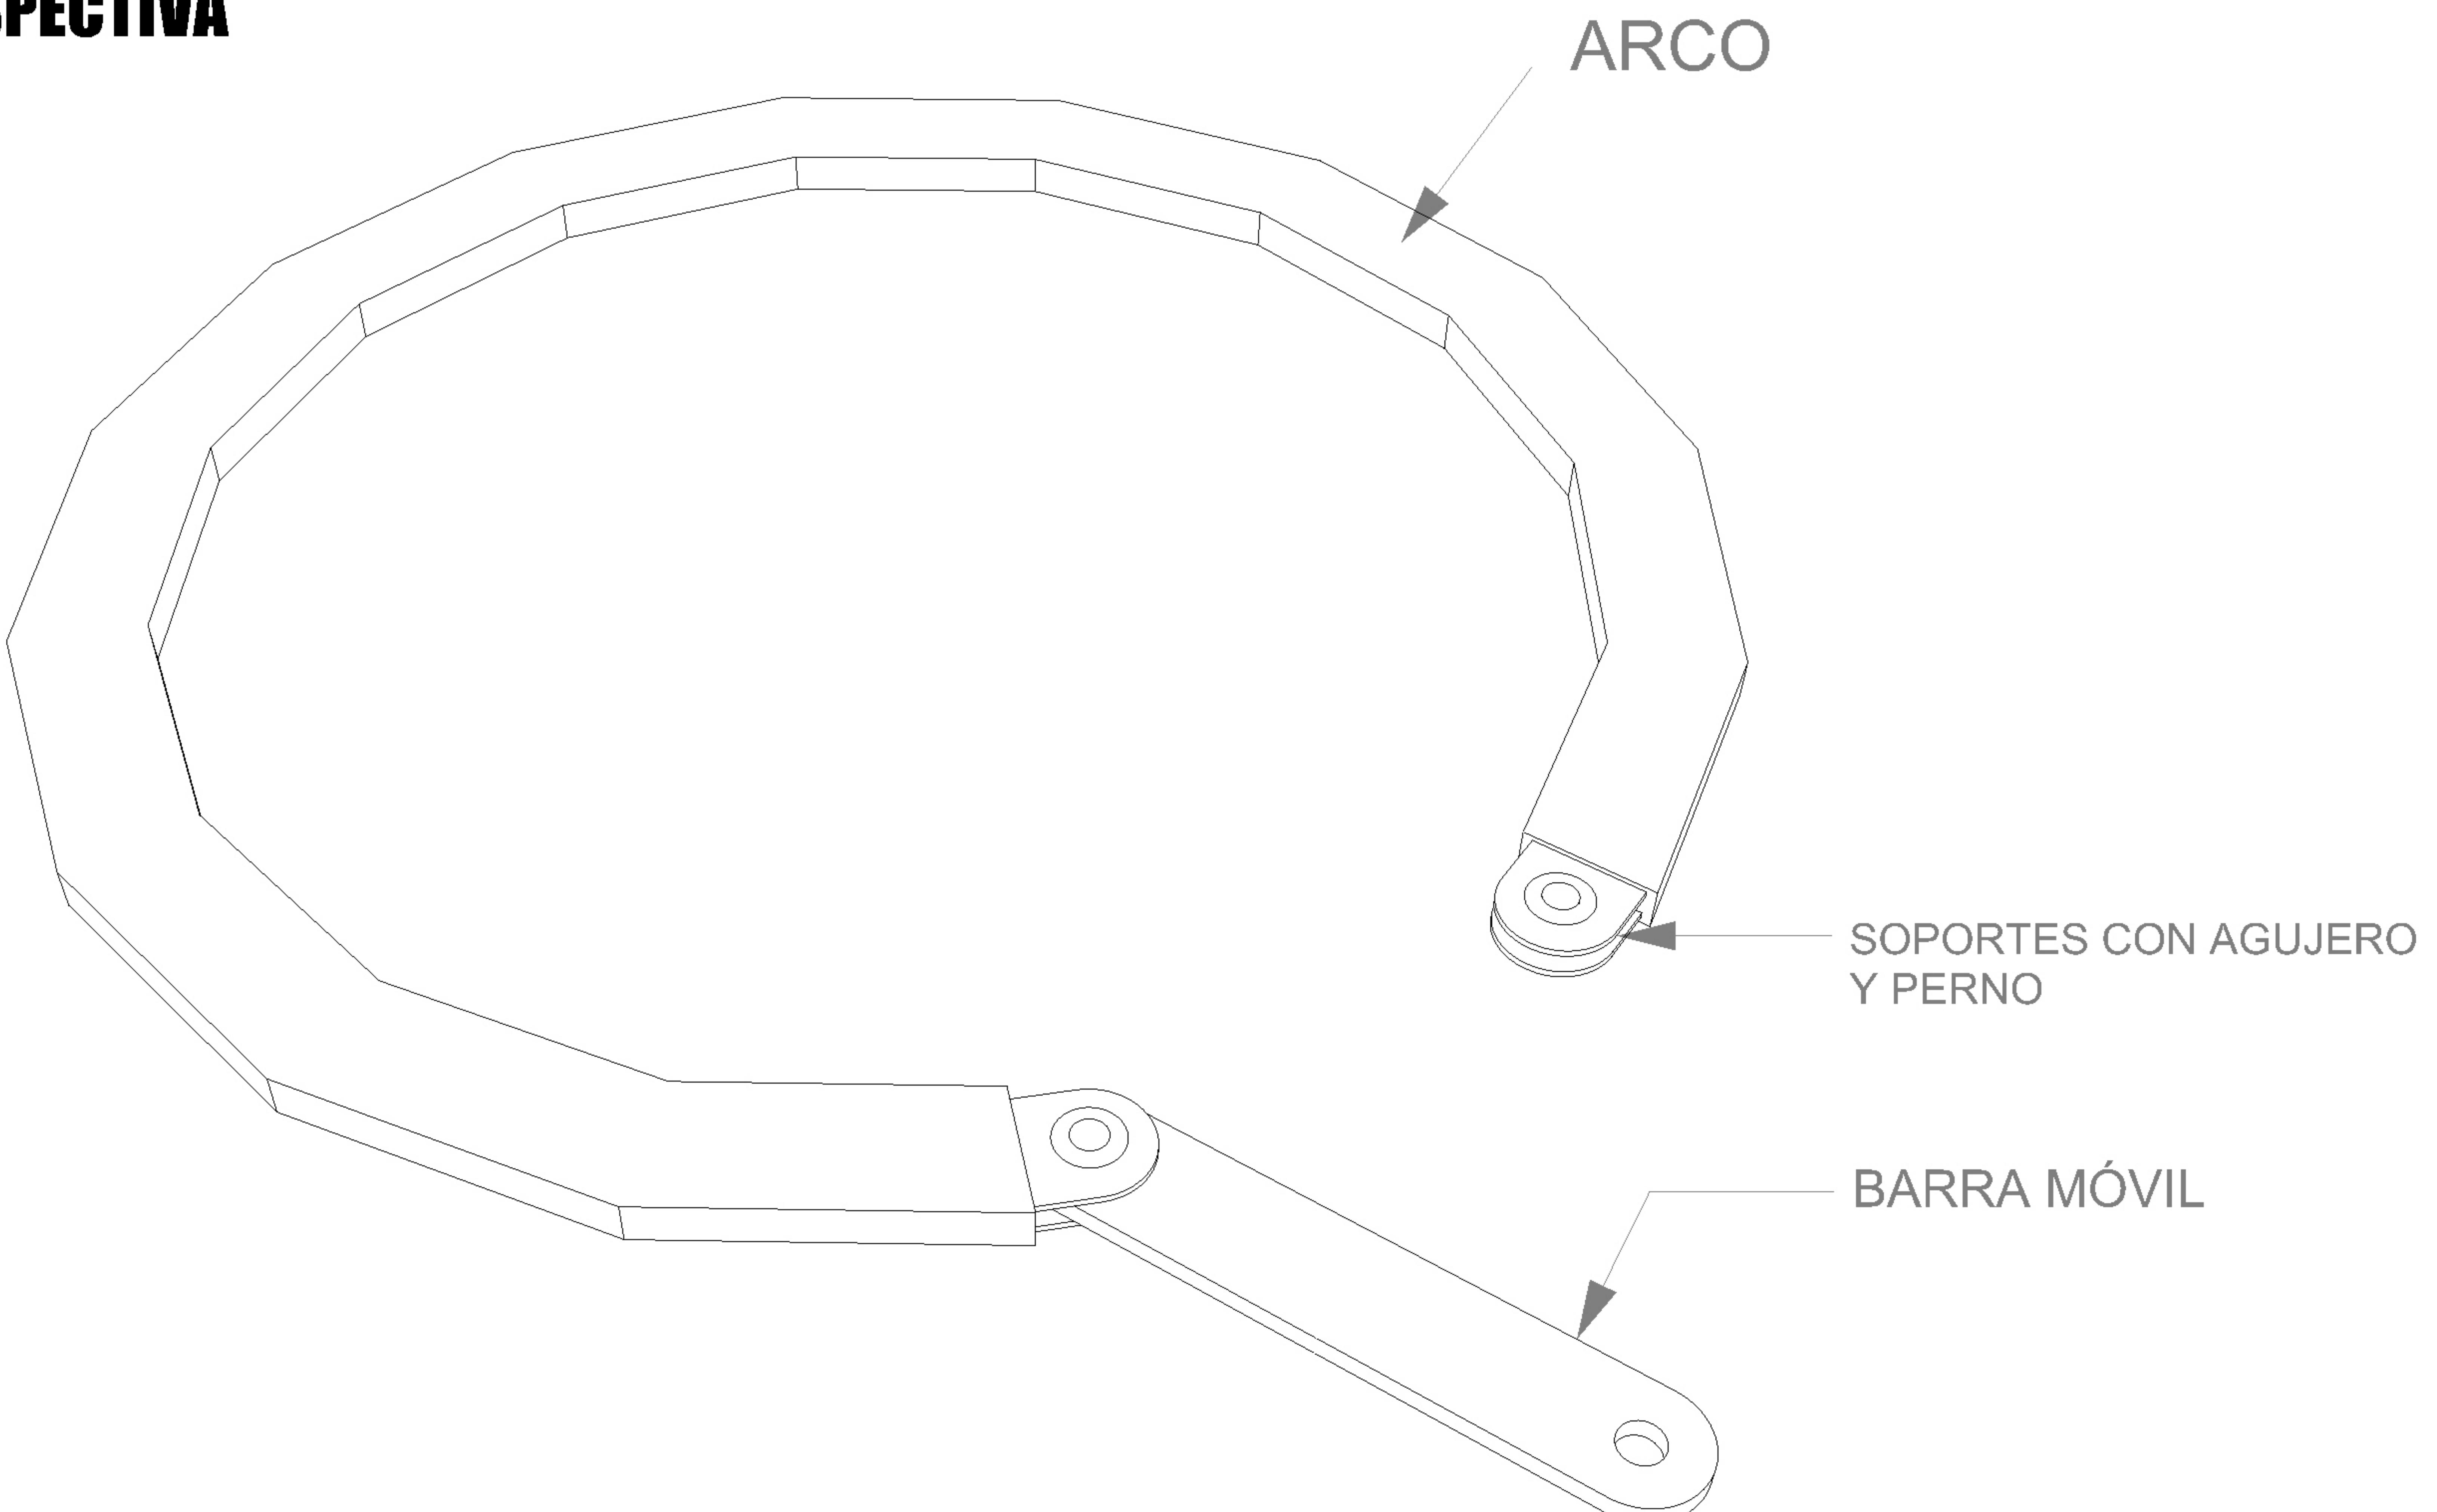

PROYECTO_Estructura caminar	DIMENSIONES GRALES: 256.00 x 6.50 x 246.26	ENSAMBLE GENERAL	11.MAYO.2020	
Estructura	OBSERVACIONES:		ACT. CM	
DIBUJÓ:fiscortes STUDIO	MATERIALES: ESTRUCTURA DE MDF // TRIPLEY DE 16MM CON LAMINADO PLÁSTICO O ACABADOS SEGÚN CLIENTE		ESC. -	
			HOJA -	


PLANO 6. Barra movil (x2)

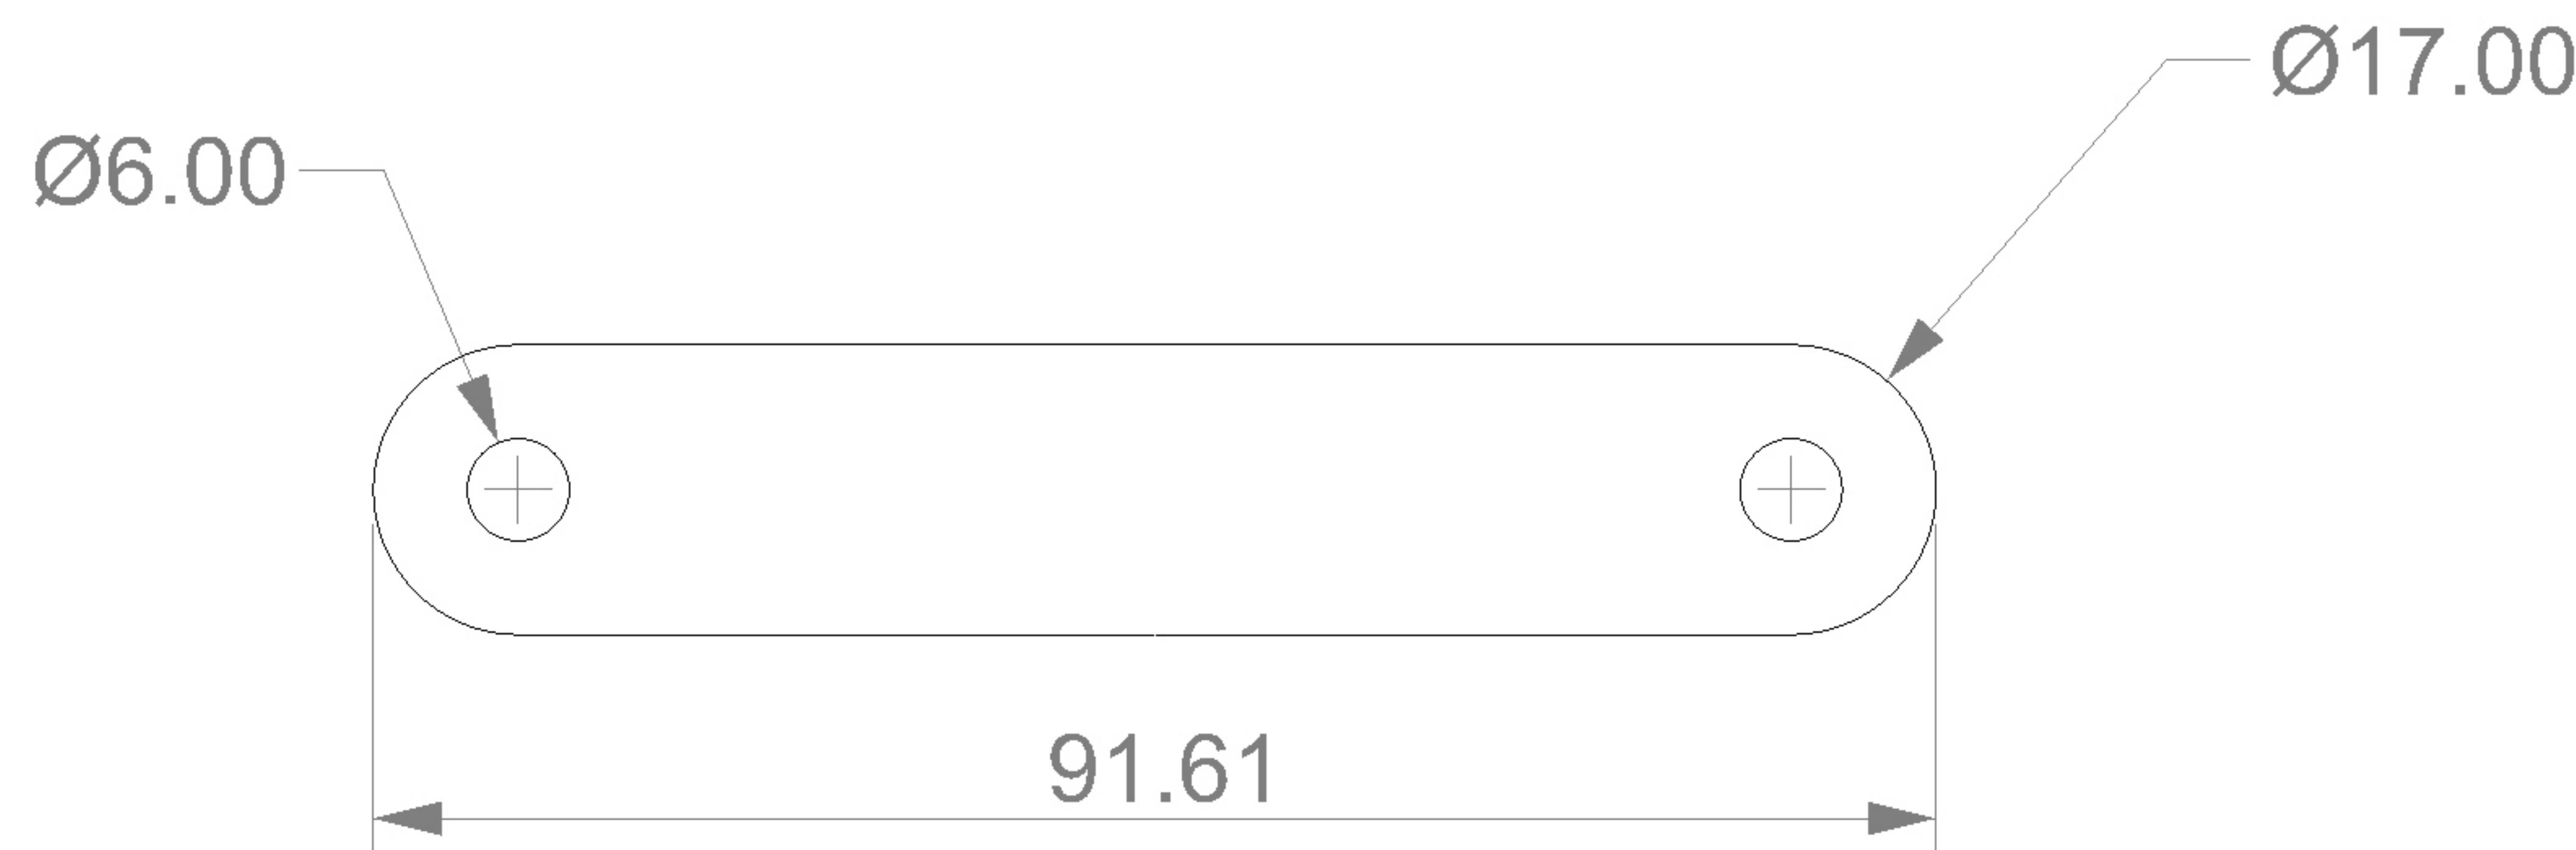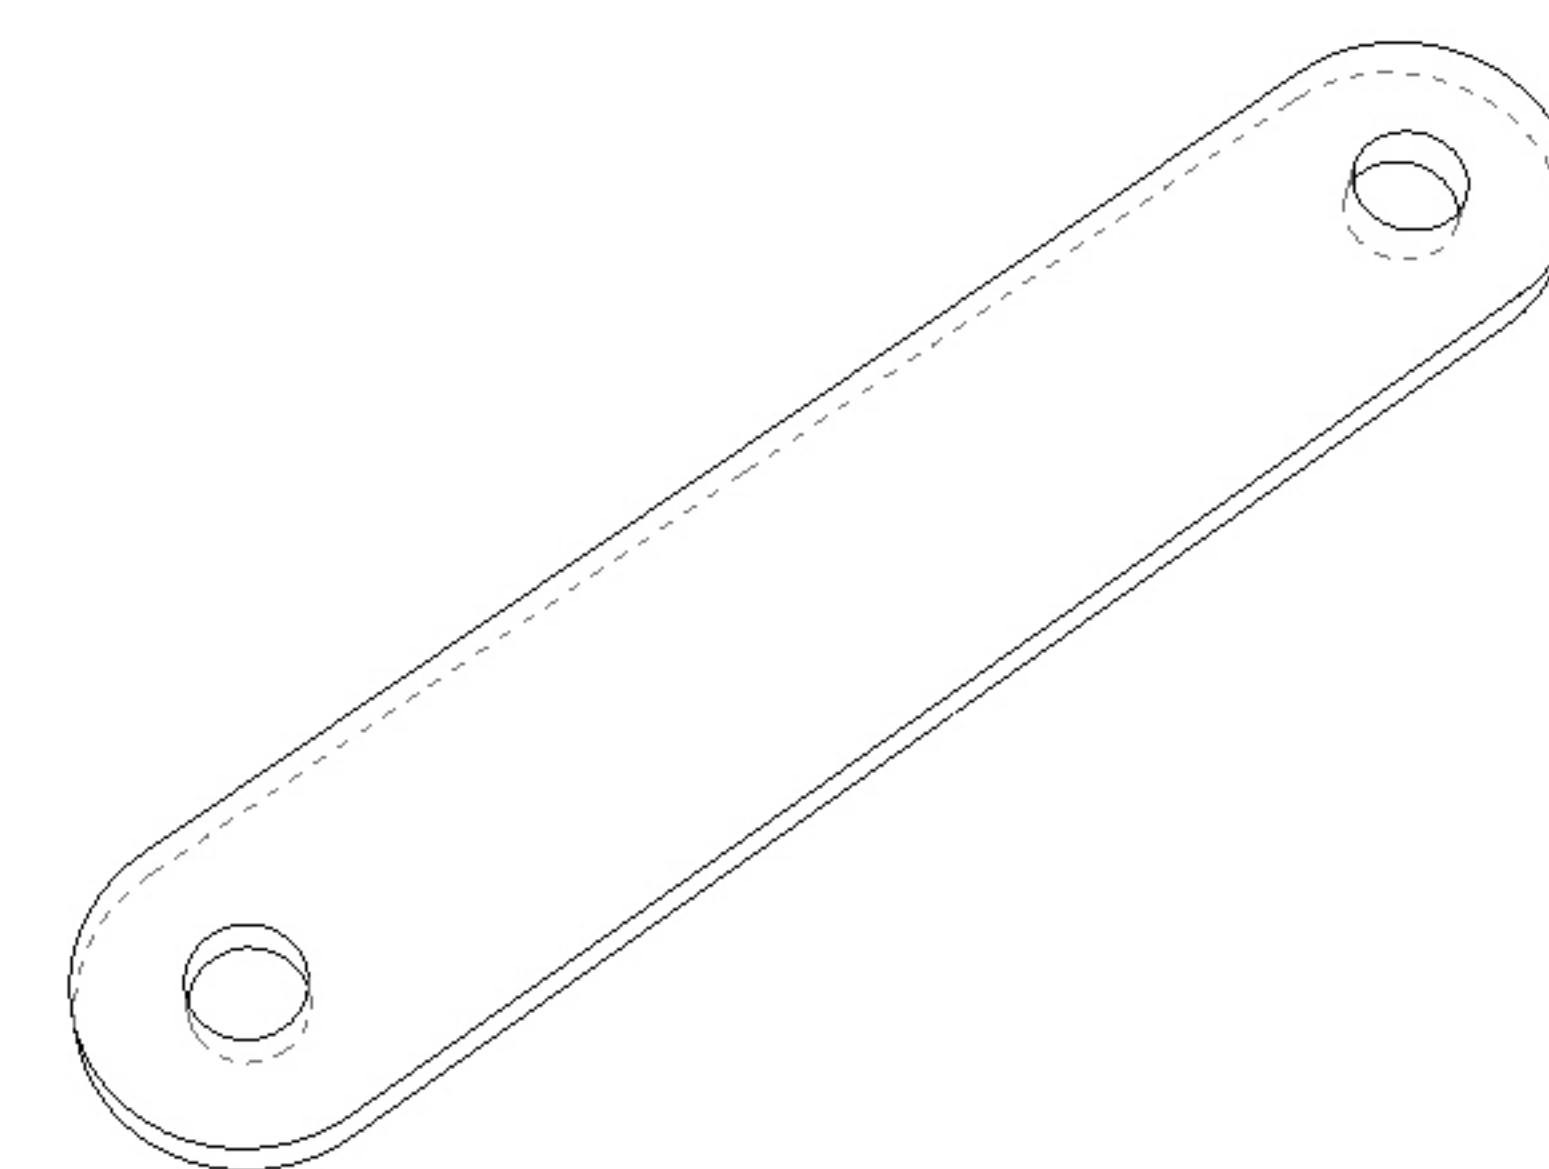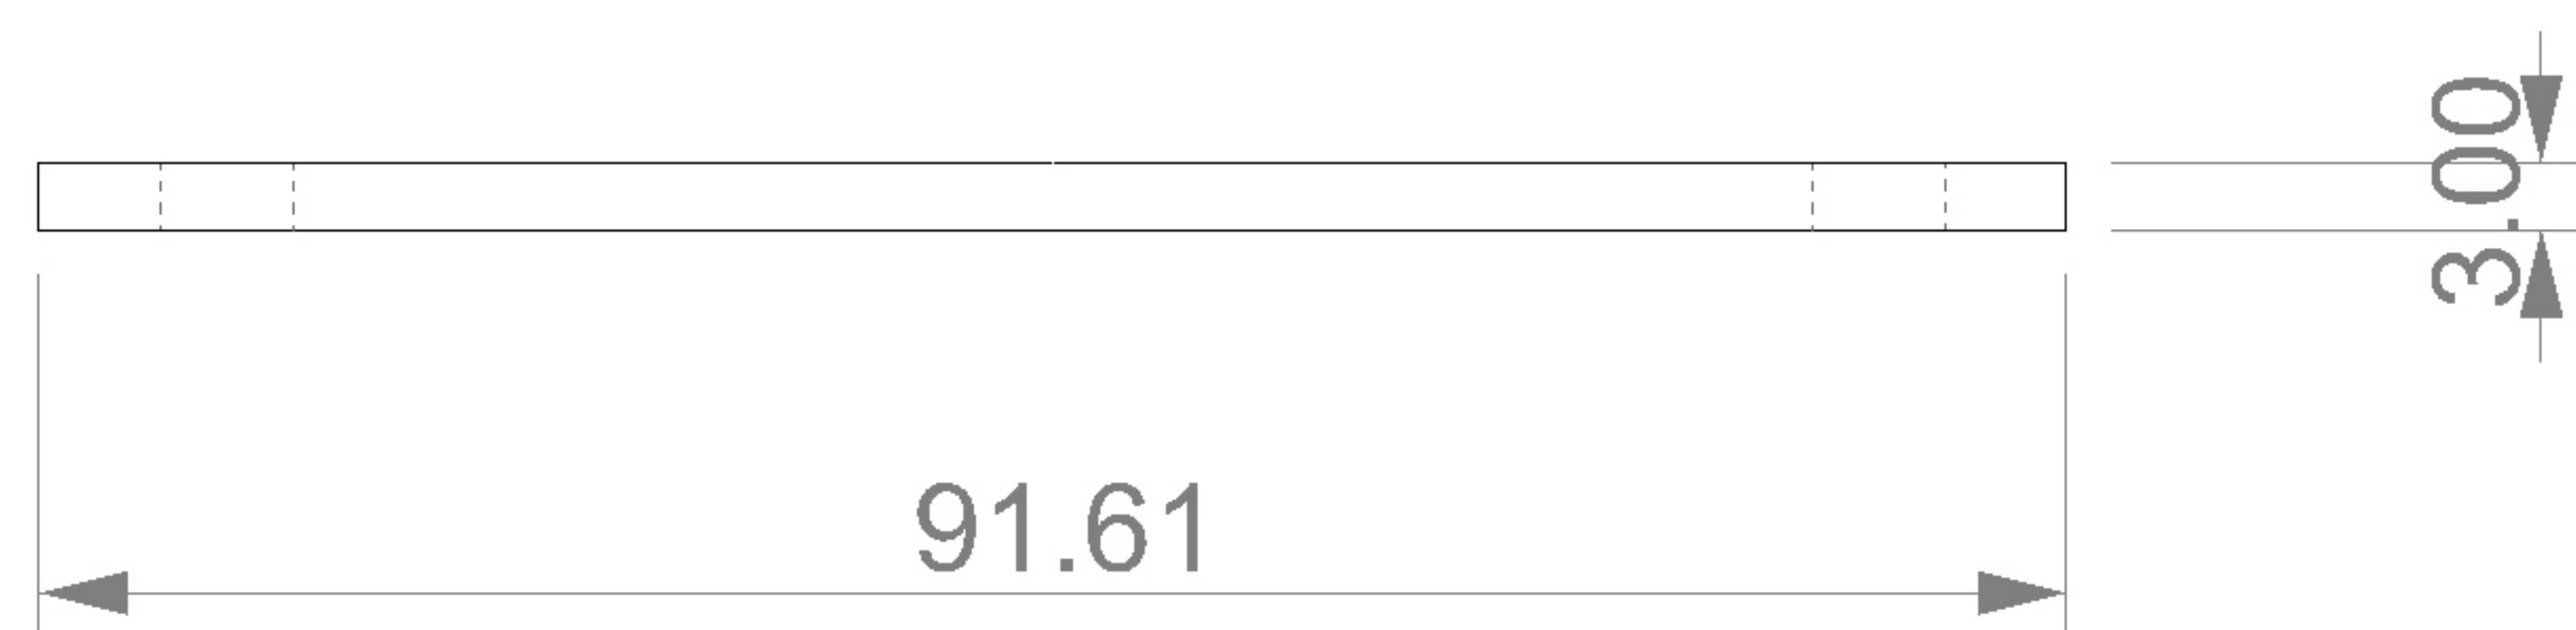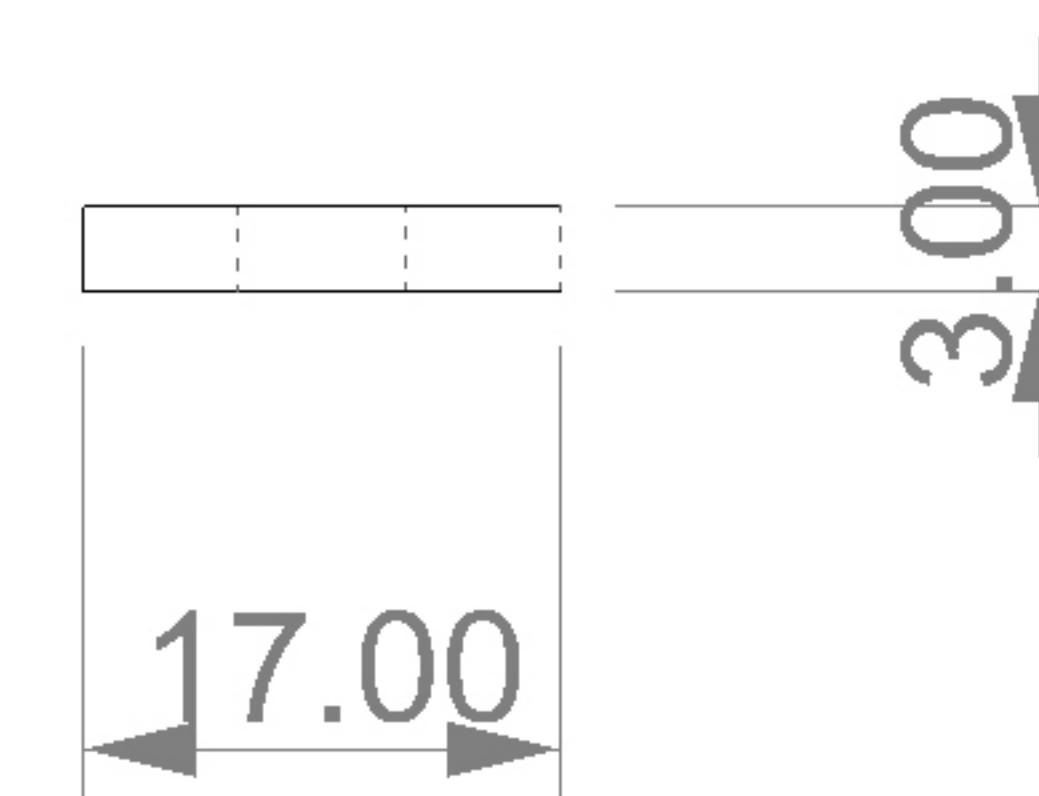VISTA SUPERIOR**VISTA PERSPECTIVA****VISTA FRONTAL****VISTA LATERAL**


PROYECTO_Estructura caminar	DIMENSIONES GRALES: 91.61 x 3.00 x 17.00	ENSAMBLE GENERAL	11.MAYO.2020	
Estructura	OBSERVACIONES:		ACT. CM	
DIBUJÓ:fiscortes STUDIO	MATERIALES: ESTRUCTURA DE MDF // TRIPLEY DE 16MM CON LAMINADO PLÁSTICO O ACABADOS SEGÚN CLIENTE		ESC. -	
			HOJA -	

PLANO 7. Soportes para Barra móvil (x 4 pares)


VISTA SUPERIOR

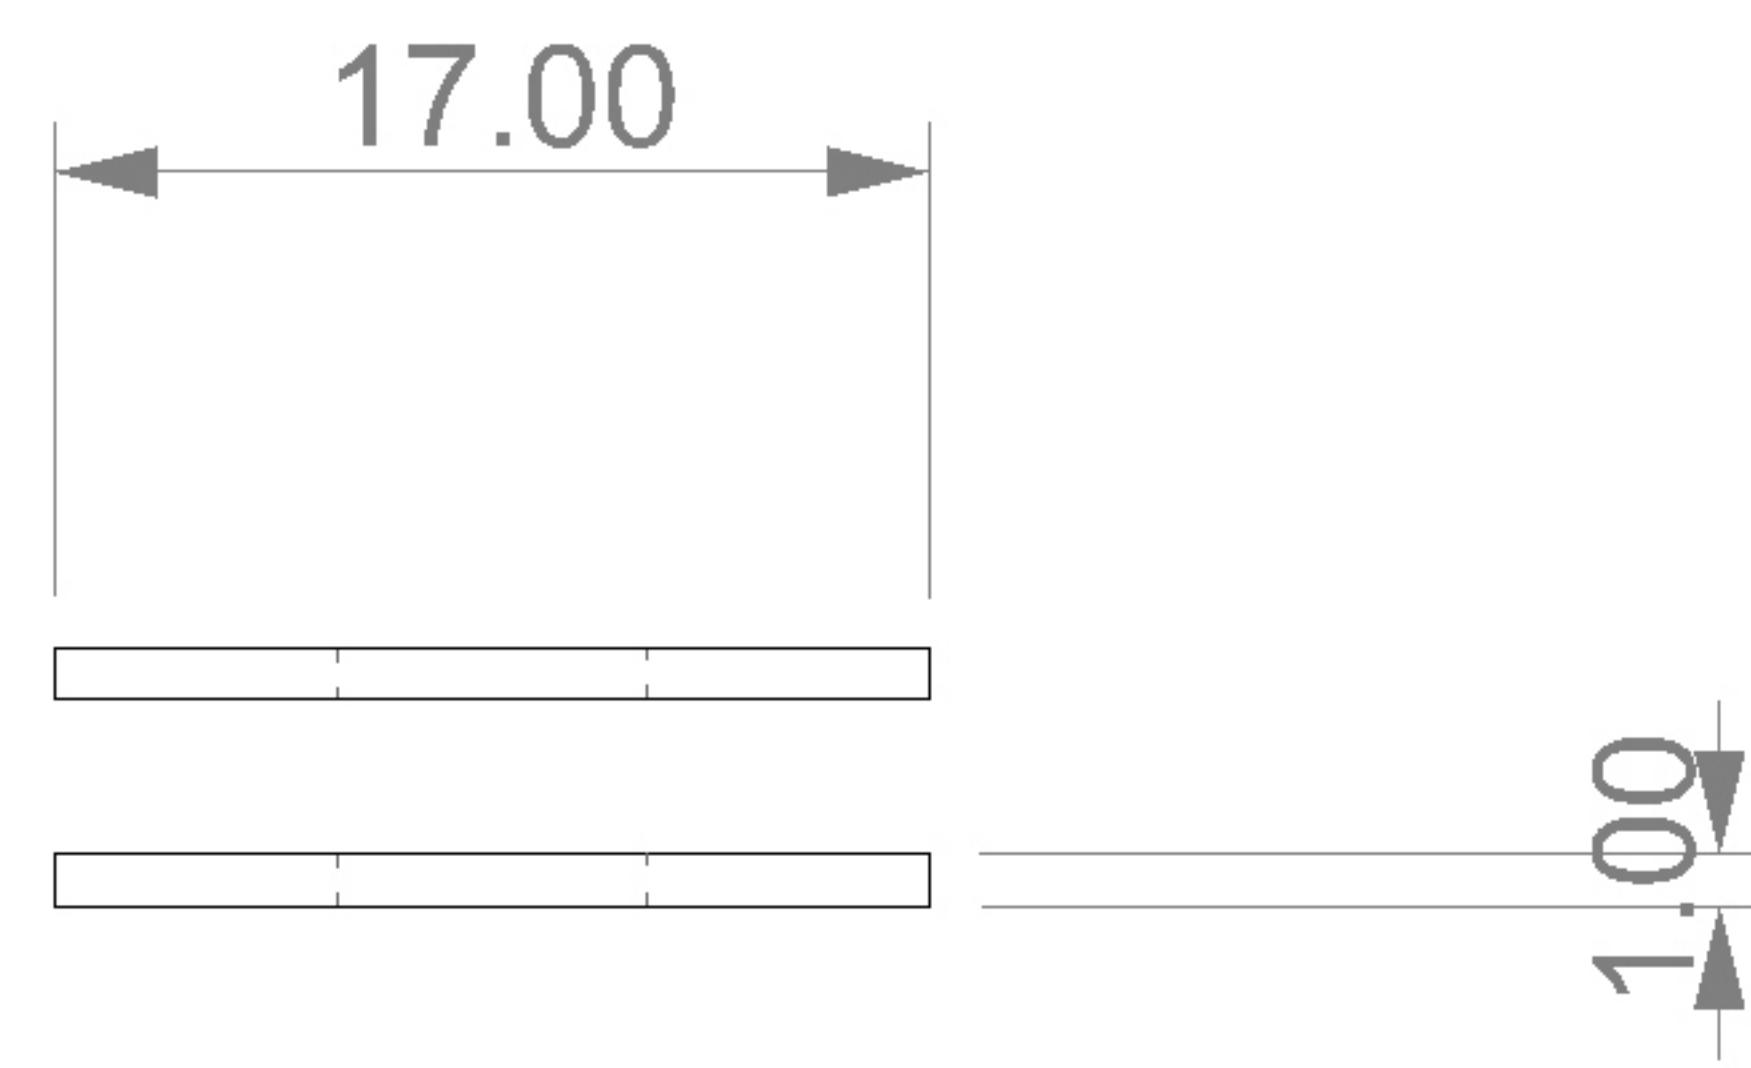


VISTA PERSPECTIVA

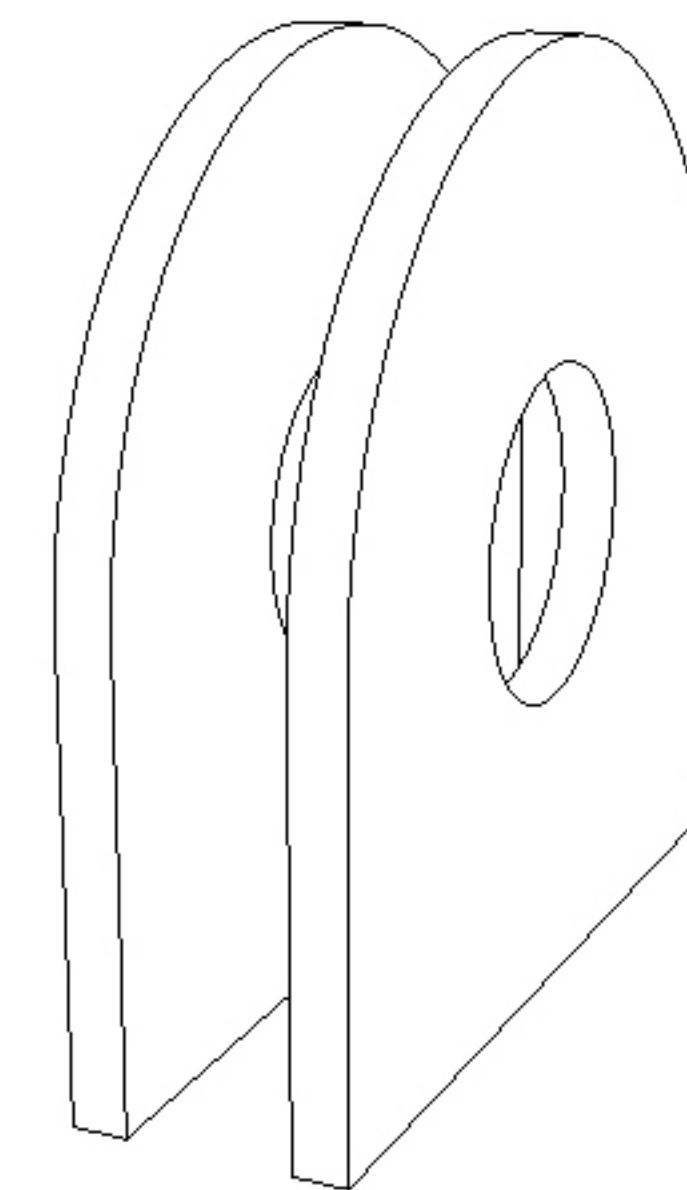

VISTA FRONTAL

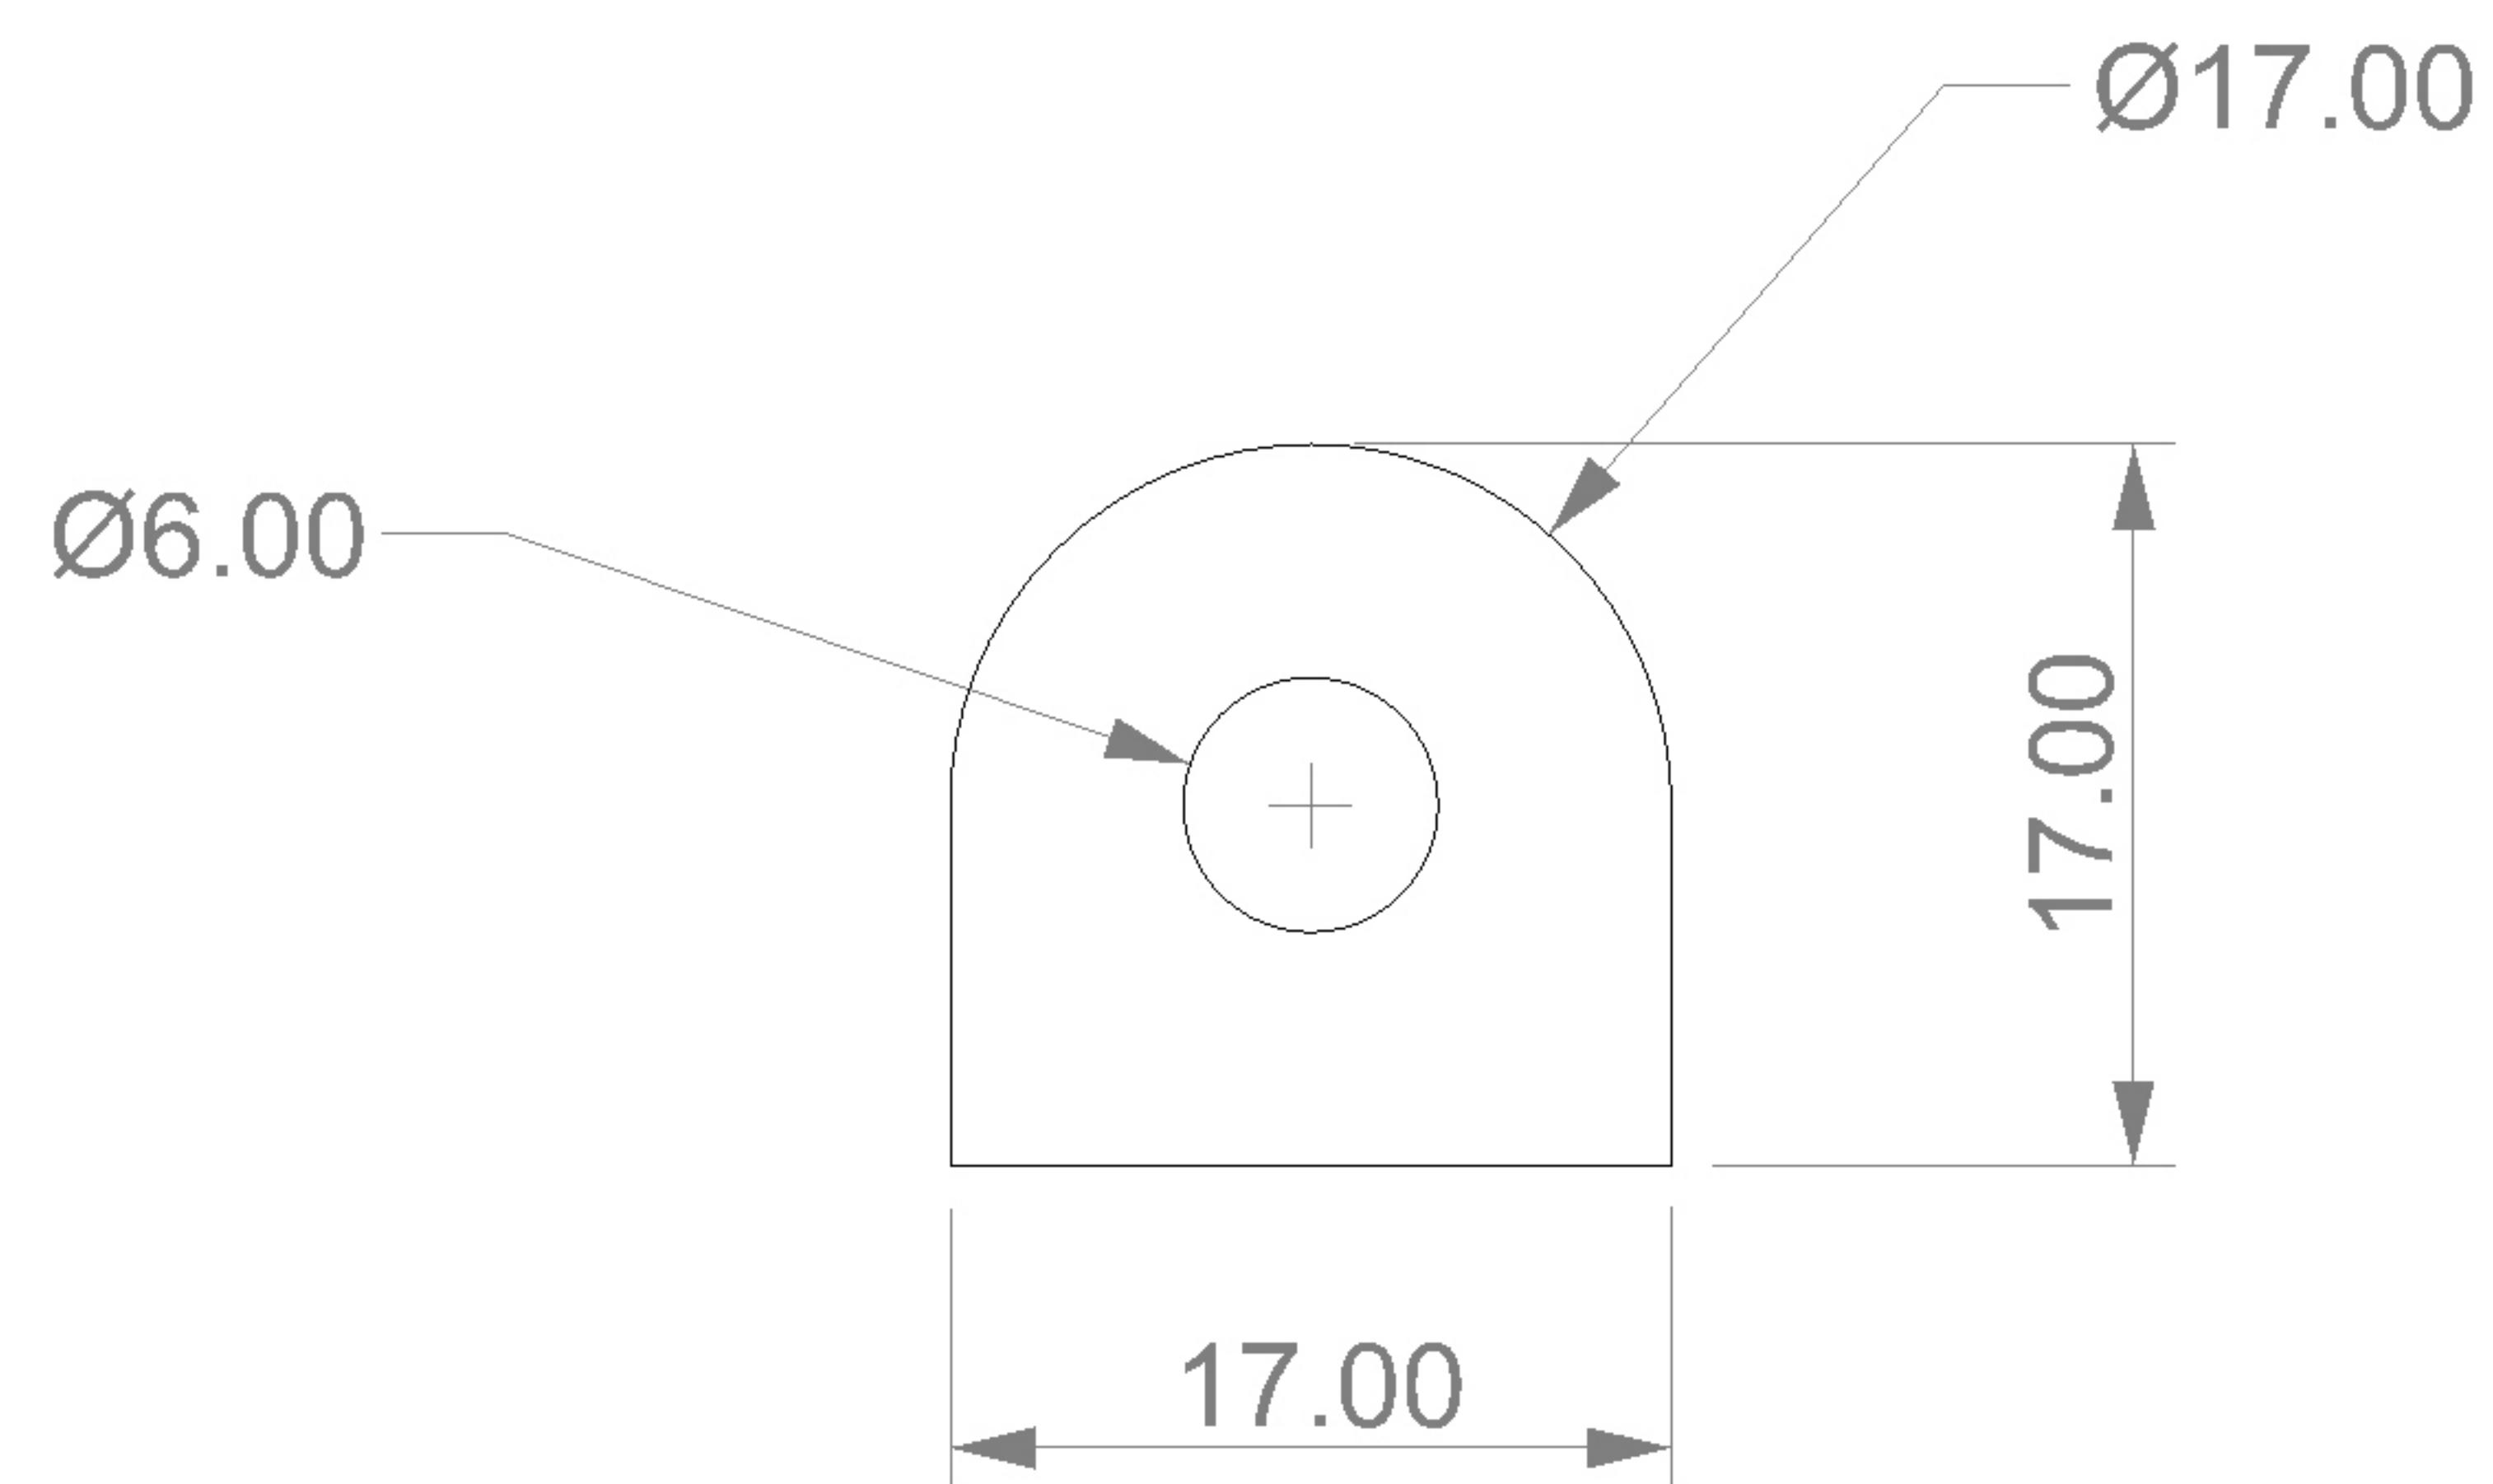


VISTA LATERAL

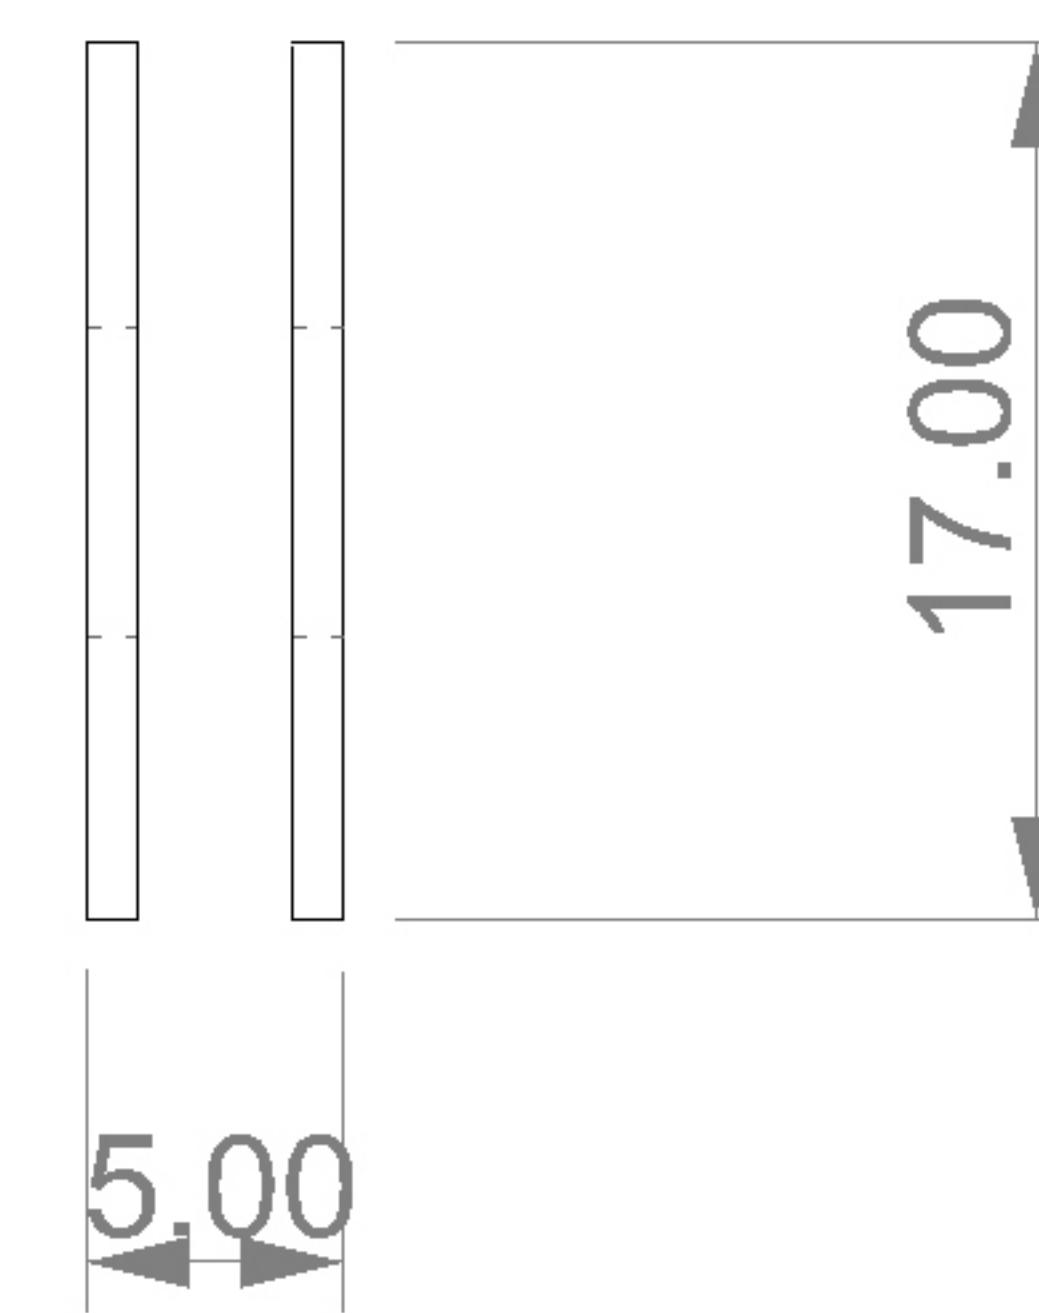


PROYECTO_Estructura caminar	DIMENSIONES GRALES: 17.00 x 17.00 x 5.00	ENSAMBLE GENERAL	11.MAYO.2020	
Estructura	OBSERVACIONES:		ACT. CM	
DIBUJÓ:fiscortes STUDIO	MATERIALES: ESTRUCTURA DE MDF // TRIPLEY DE 16MM CON LAMINADO PLÁSTICO O ACABADOS SEGÚN CLIENTE		ESC. -	
			HOJA -	

PLANO 8. Travesaños x 14


VISTA SUPERIOR

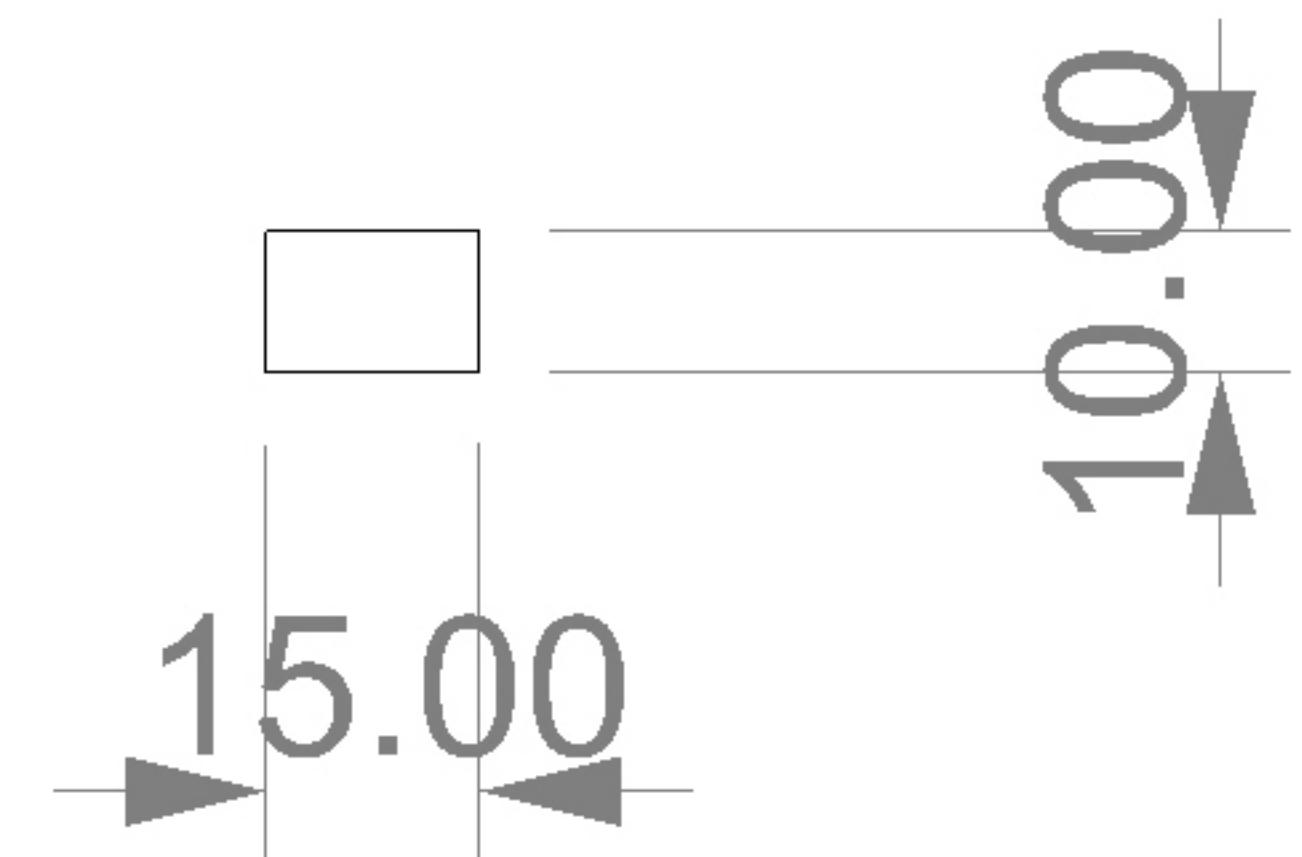


VISTA PERSPECTIVA

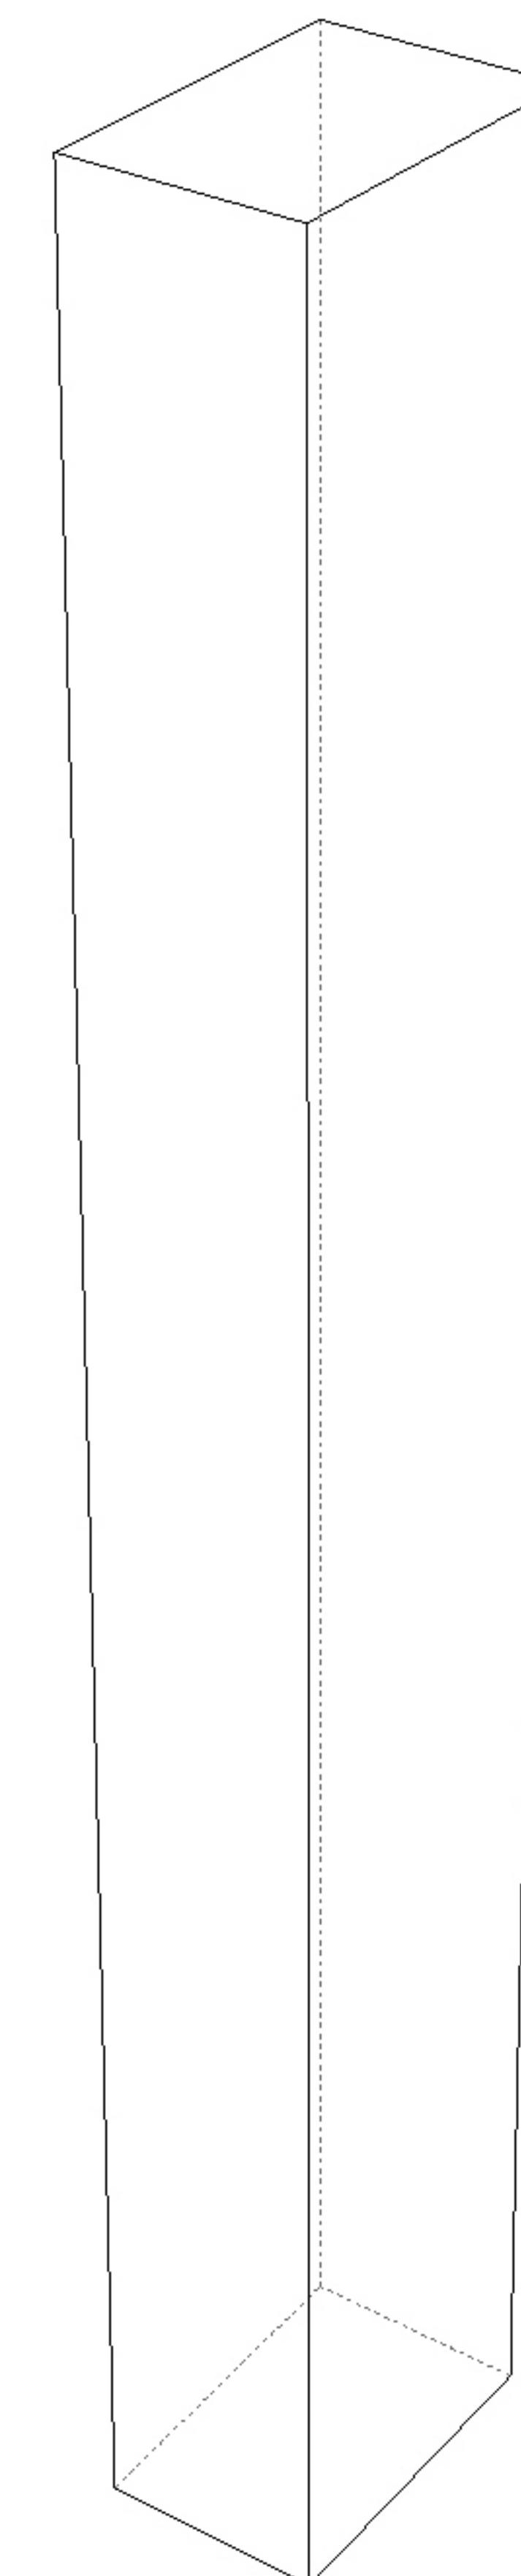


VISTA FRONTAL

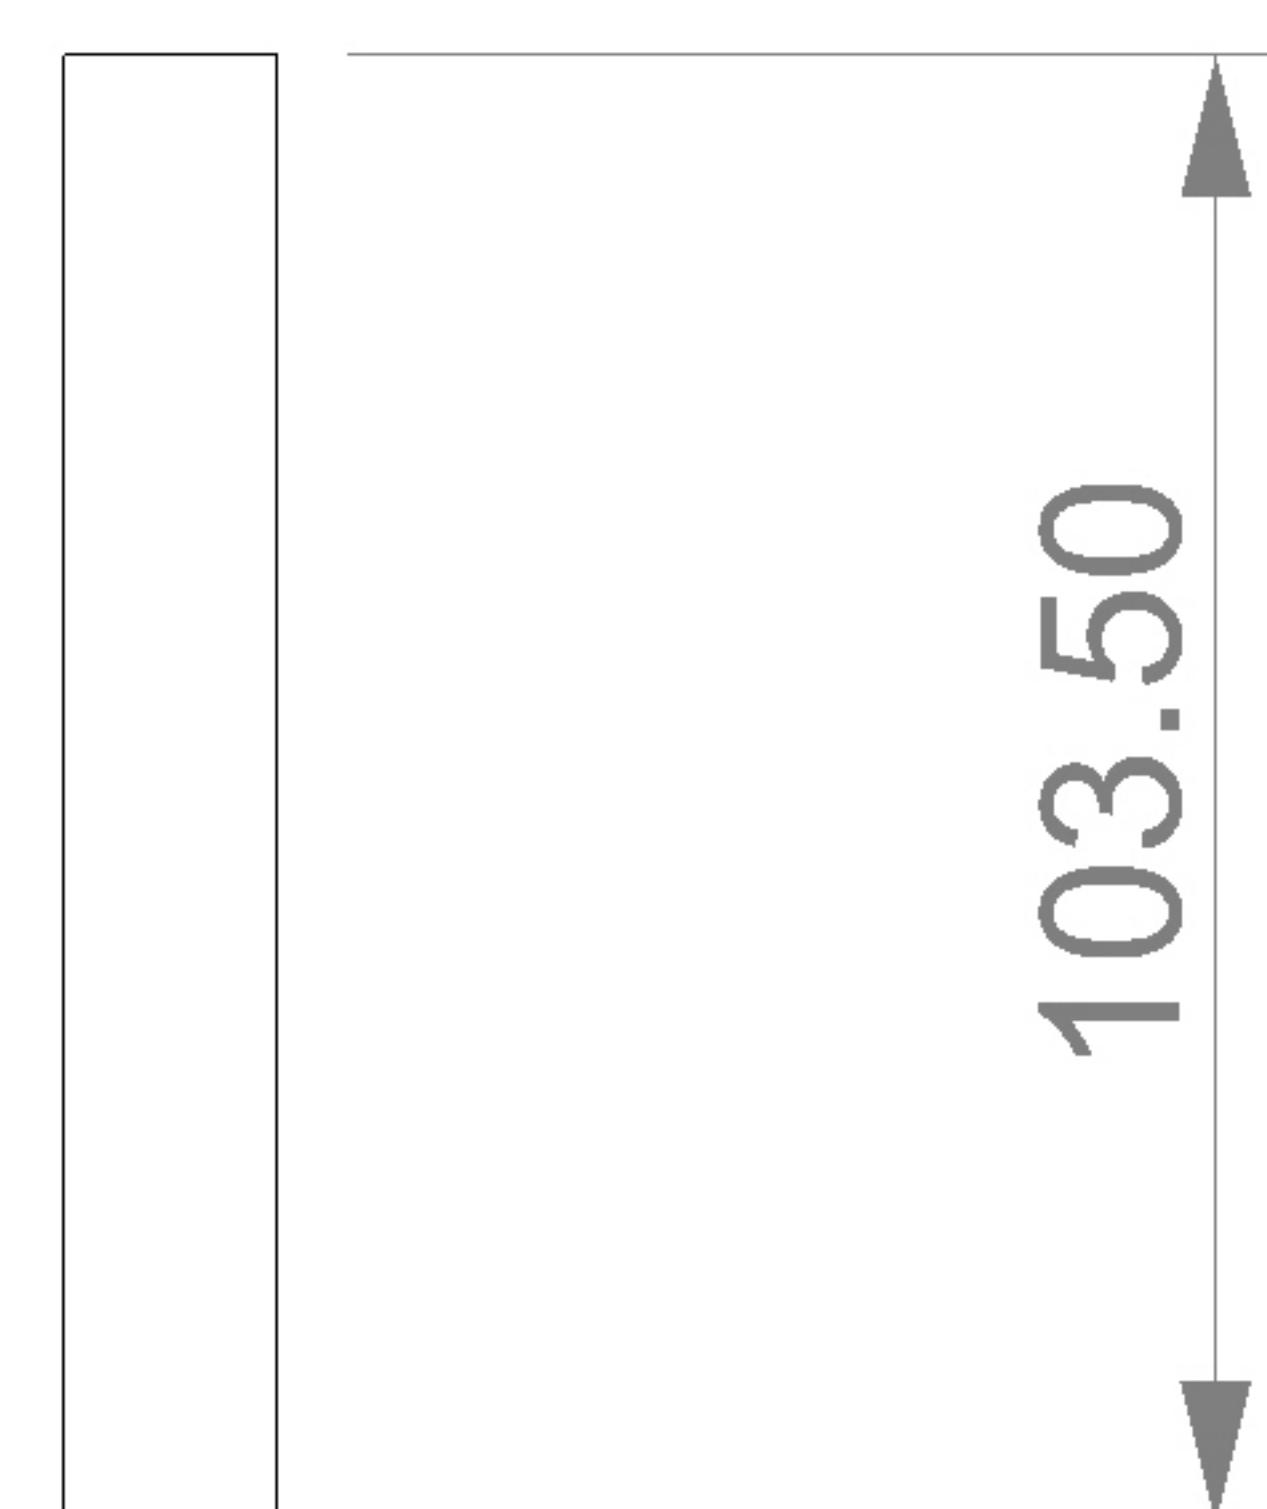

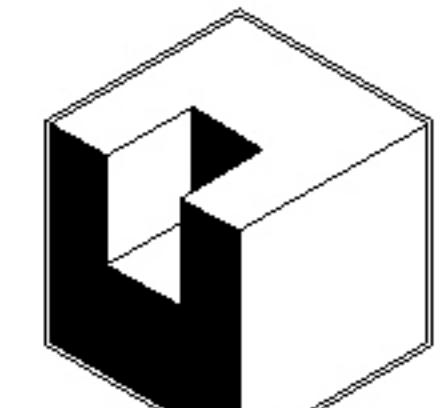
PROYECTO_Estructura caminar	DIMENSIONES GRALES: 15.00 x 103.5 x 10.00	ENSAMBLE GENERAL	11.MAYO.2020	
Estructura	OBSERVACIONES:		ACT. CM	
DIBUJÓ:fiscortes STUDIO	MATERIALES: ESTRUCTURA DE MDF // TRIPLEY DE 16MM CON LAMINADO PLÁSTICO O ACABADOS SEGÚN CLIENTE		ESC. -	
			HOJA -	

PLANO 9. Base para usuarios


VISTA SUPERIOR

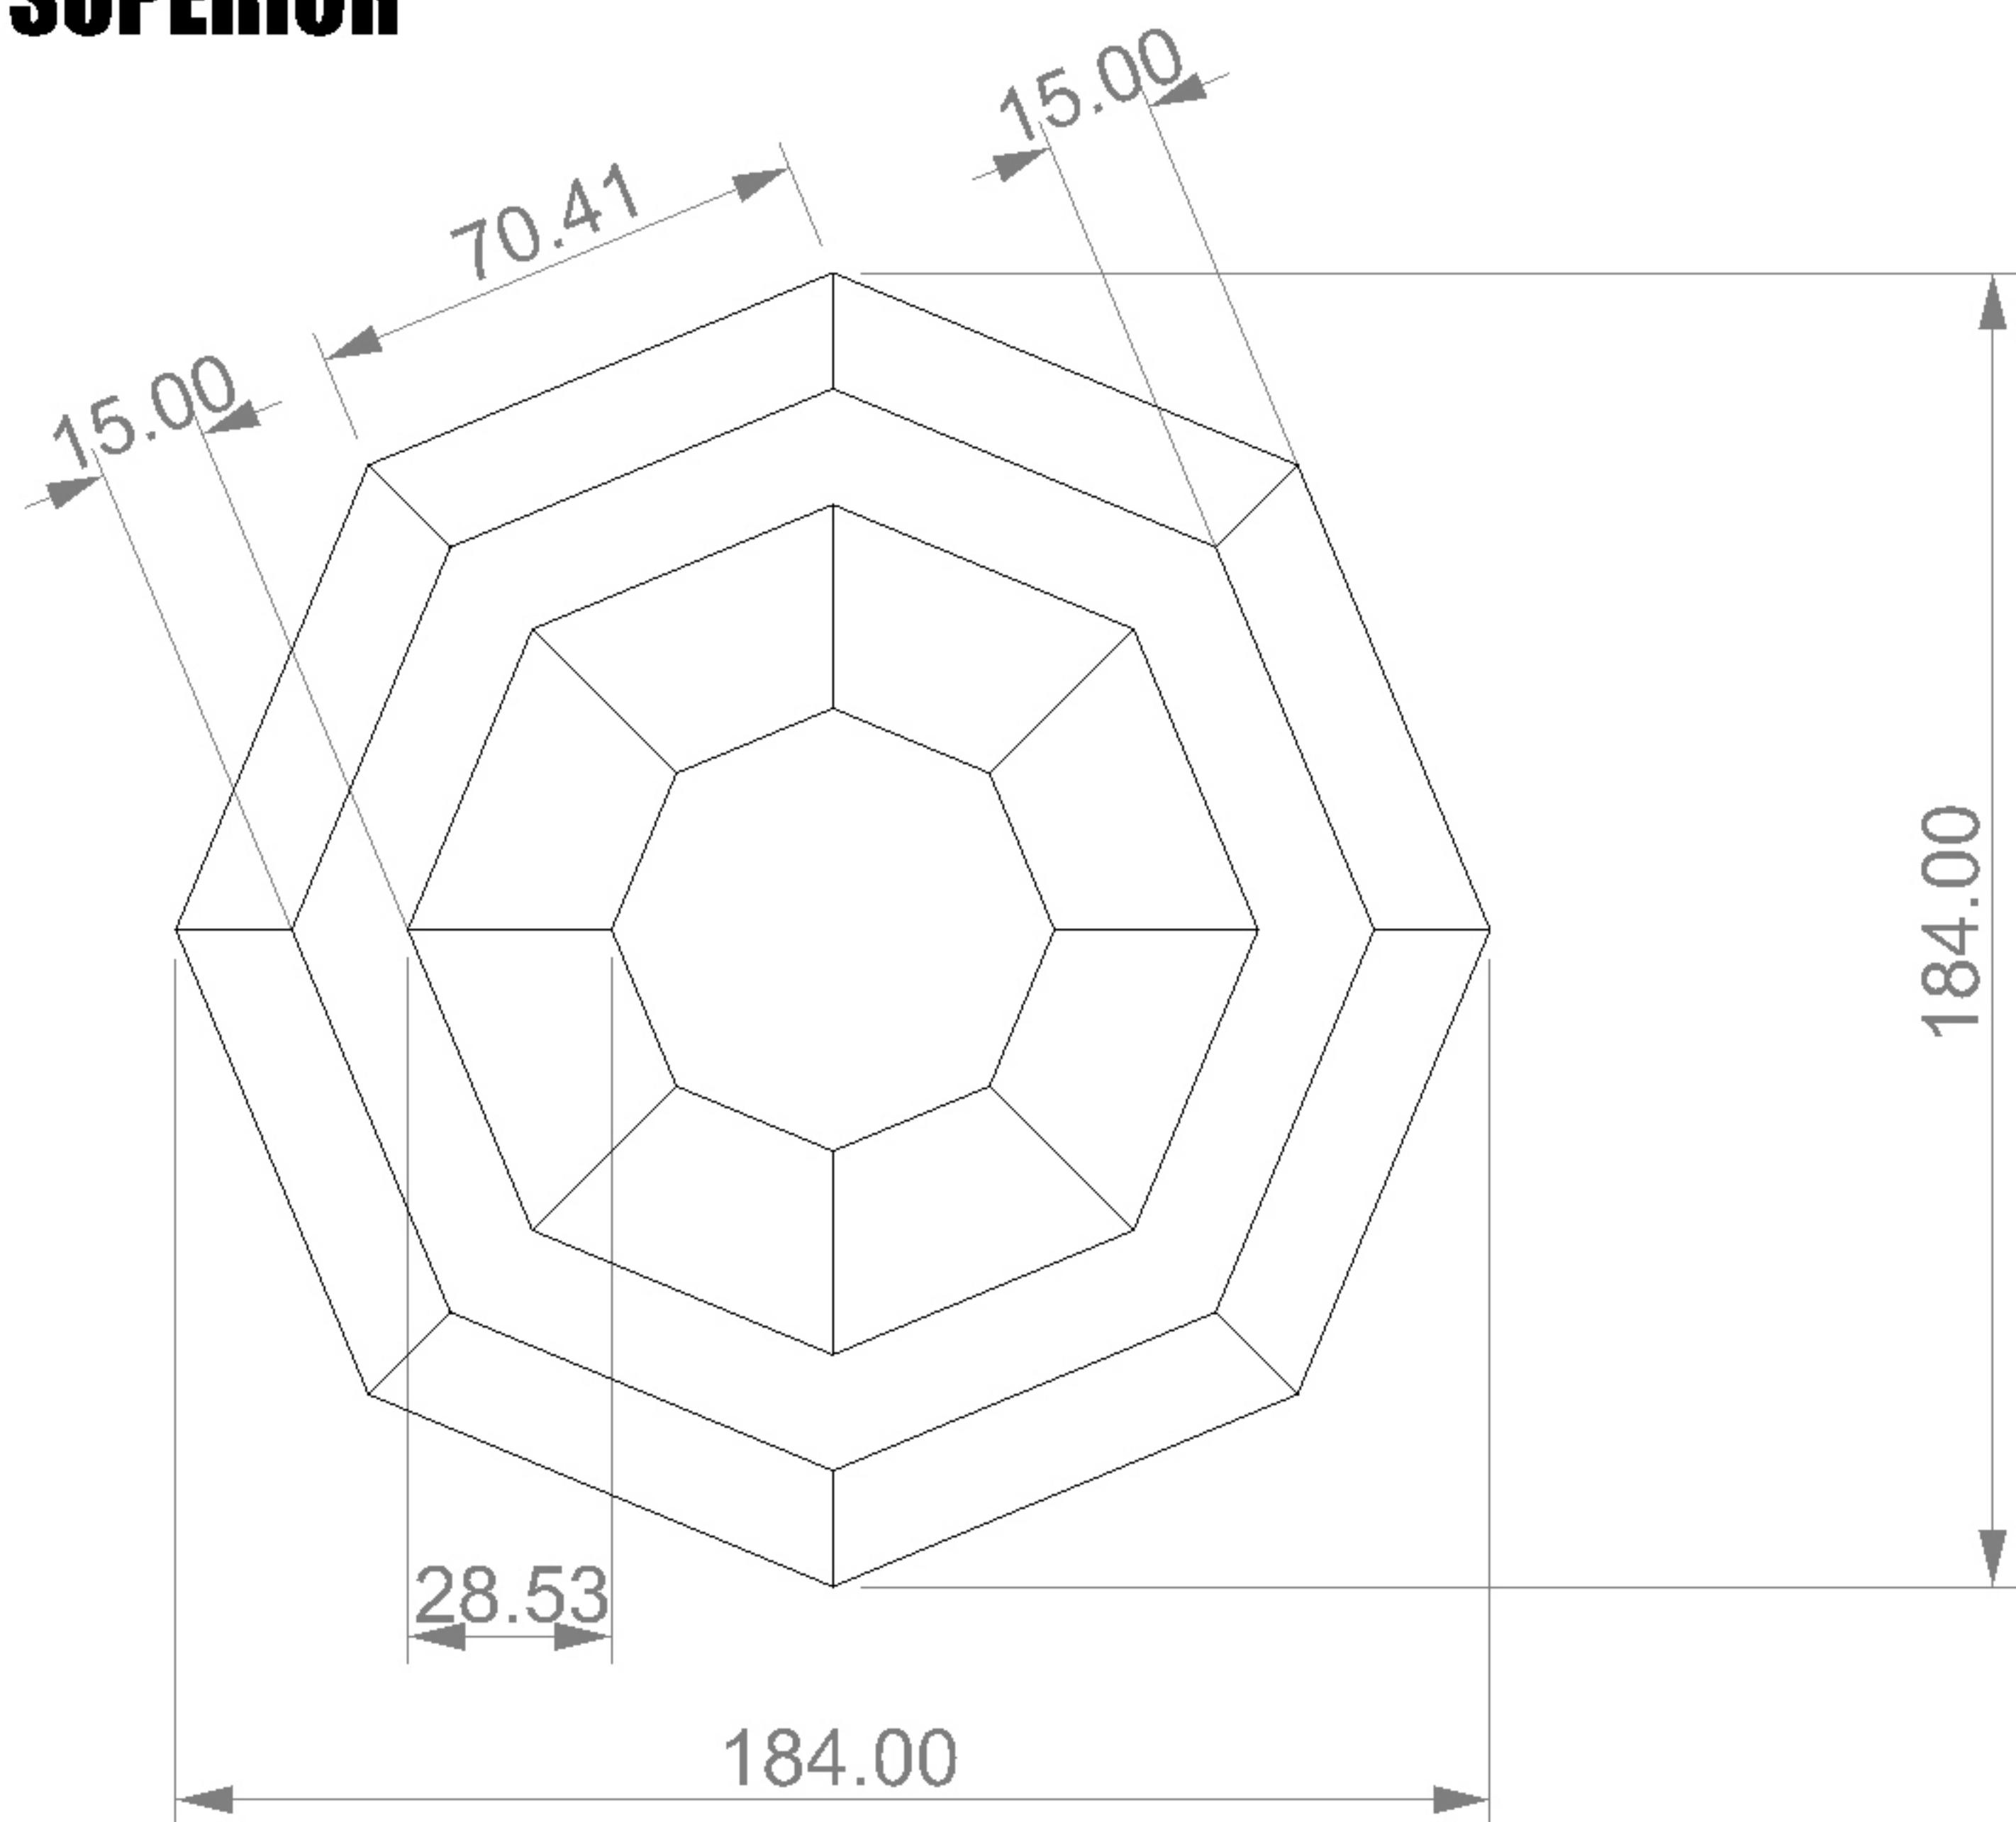


VISTA PERSPECTIVA

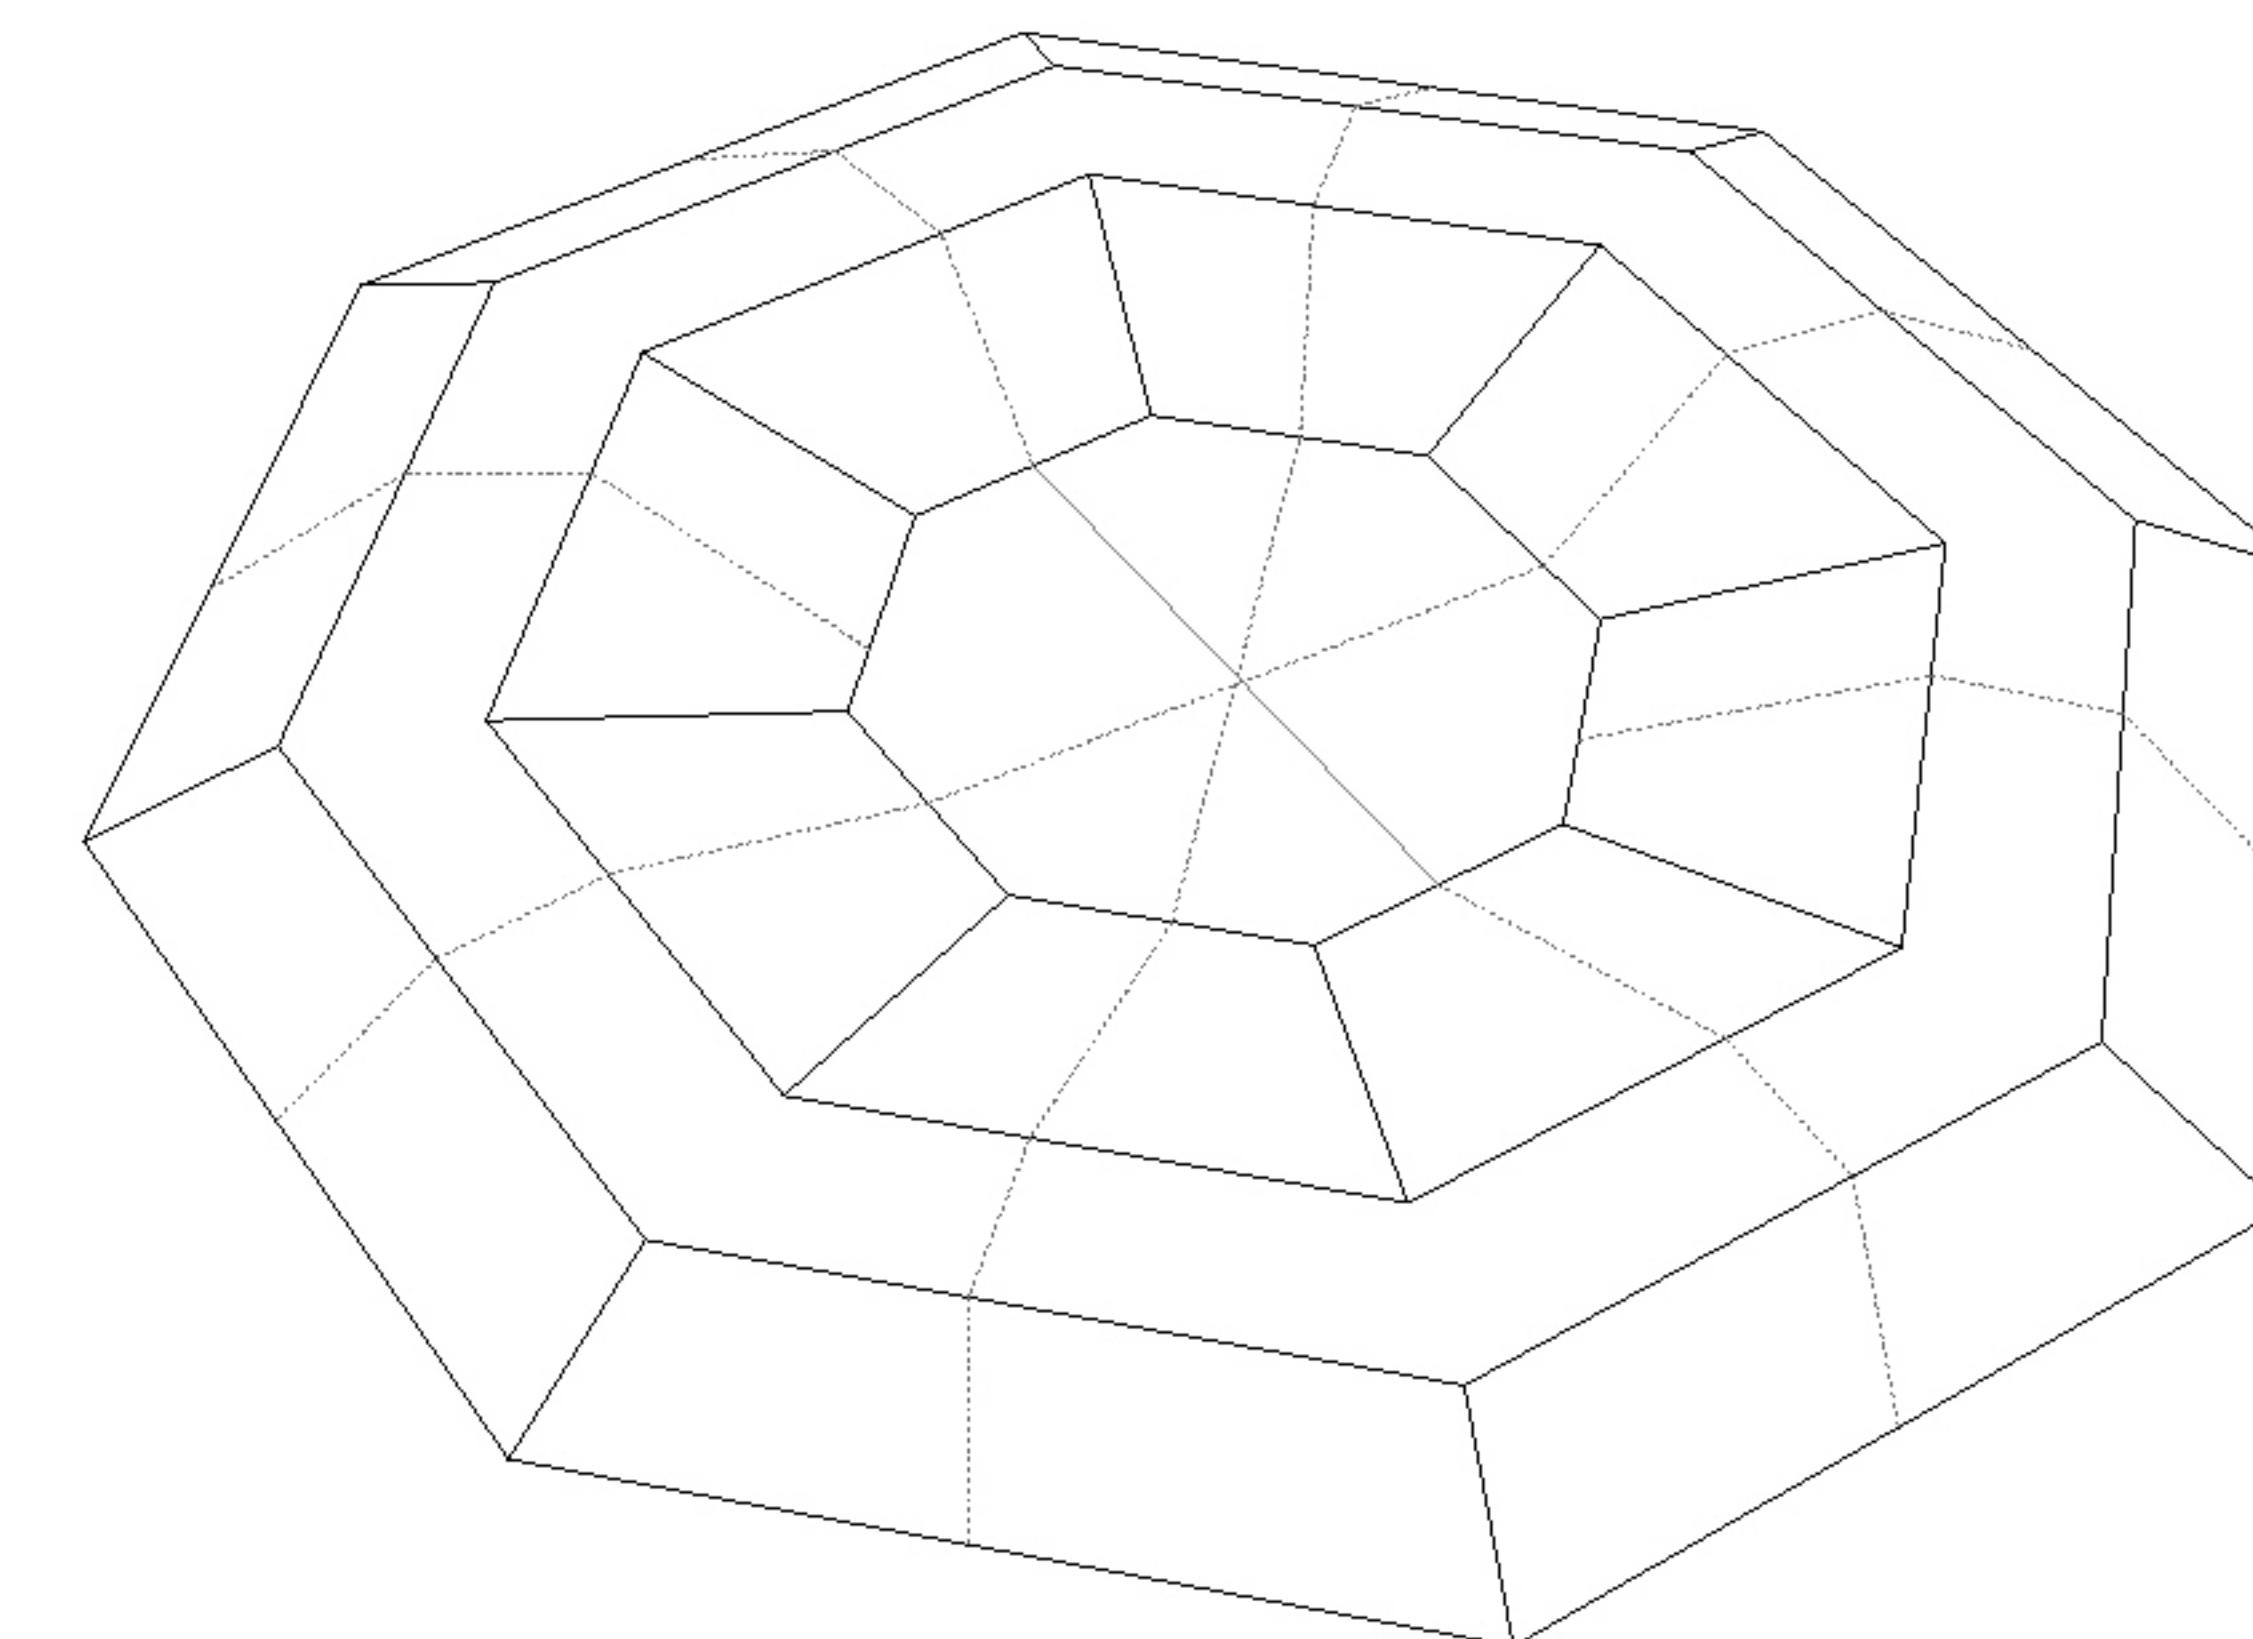

VISTA FRONTAL

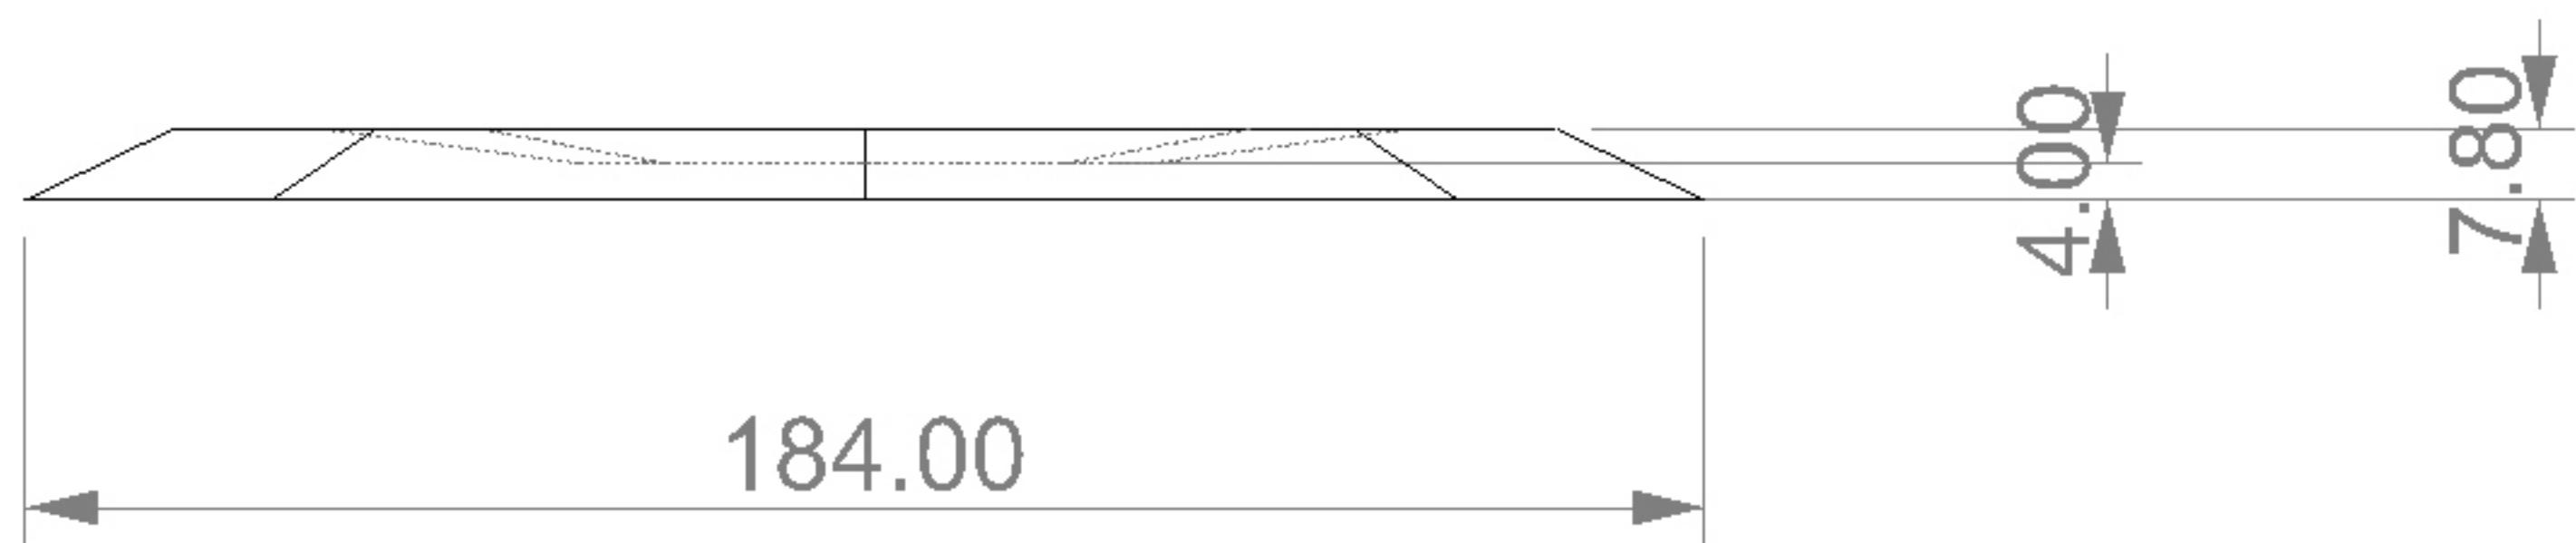


VISTA LATERAL

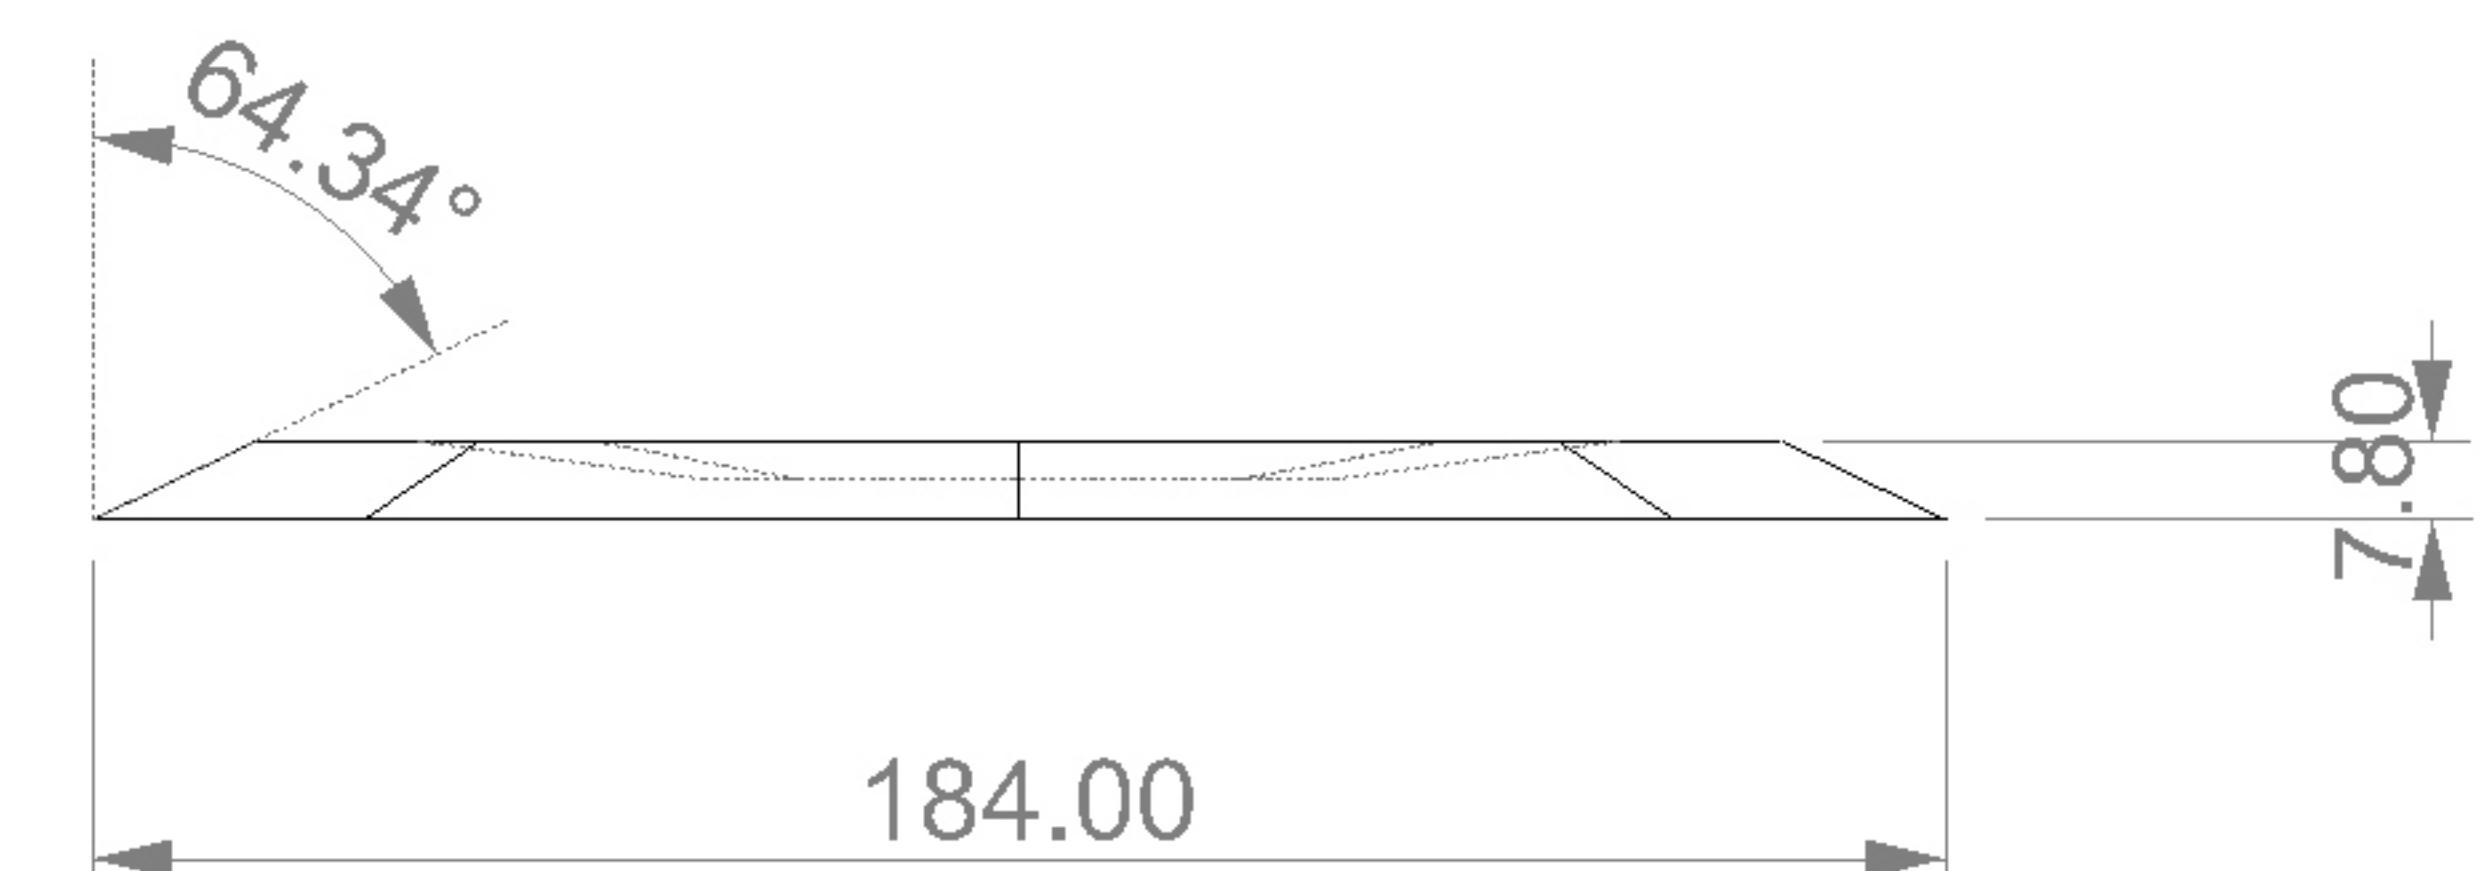


PROYECTO_Estructura caminar	DIMENSIONES GRALES: 184.00 x 7.80 x 184.00	ENSAMBLE GENERAL	11.MAYO.2020	
Estructura	OBSERVACIONES:		ACT. CM	
DIBUJÓ:fiscortes STUDIO	MATERIALES: ESTRUCTURA DE MDF // TRIPLEY DE 16MM CON LAMINADO PLÁSTICO O ACABADOS SEGÚN CLIENTE		ESC. -	
			HOJA -	

PLANO 10. Base


VISTA SUPERIOR

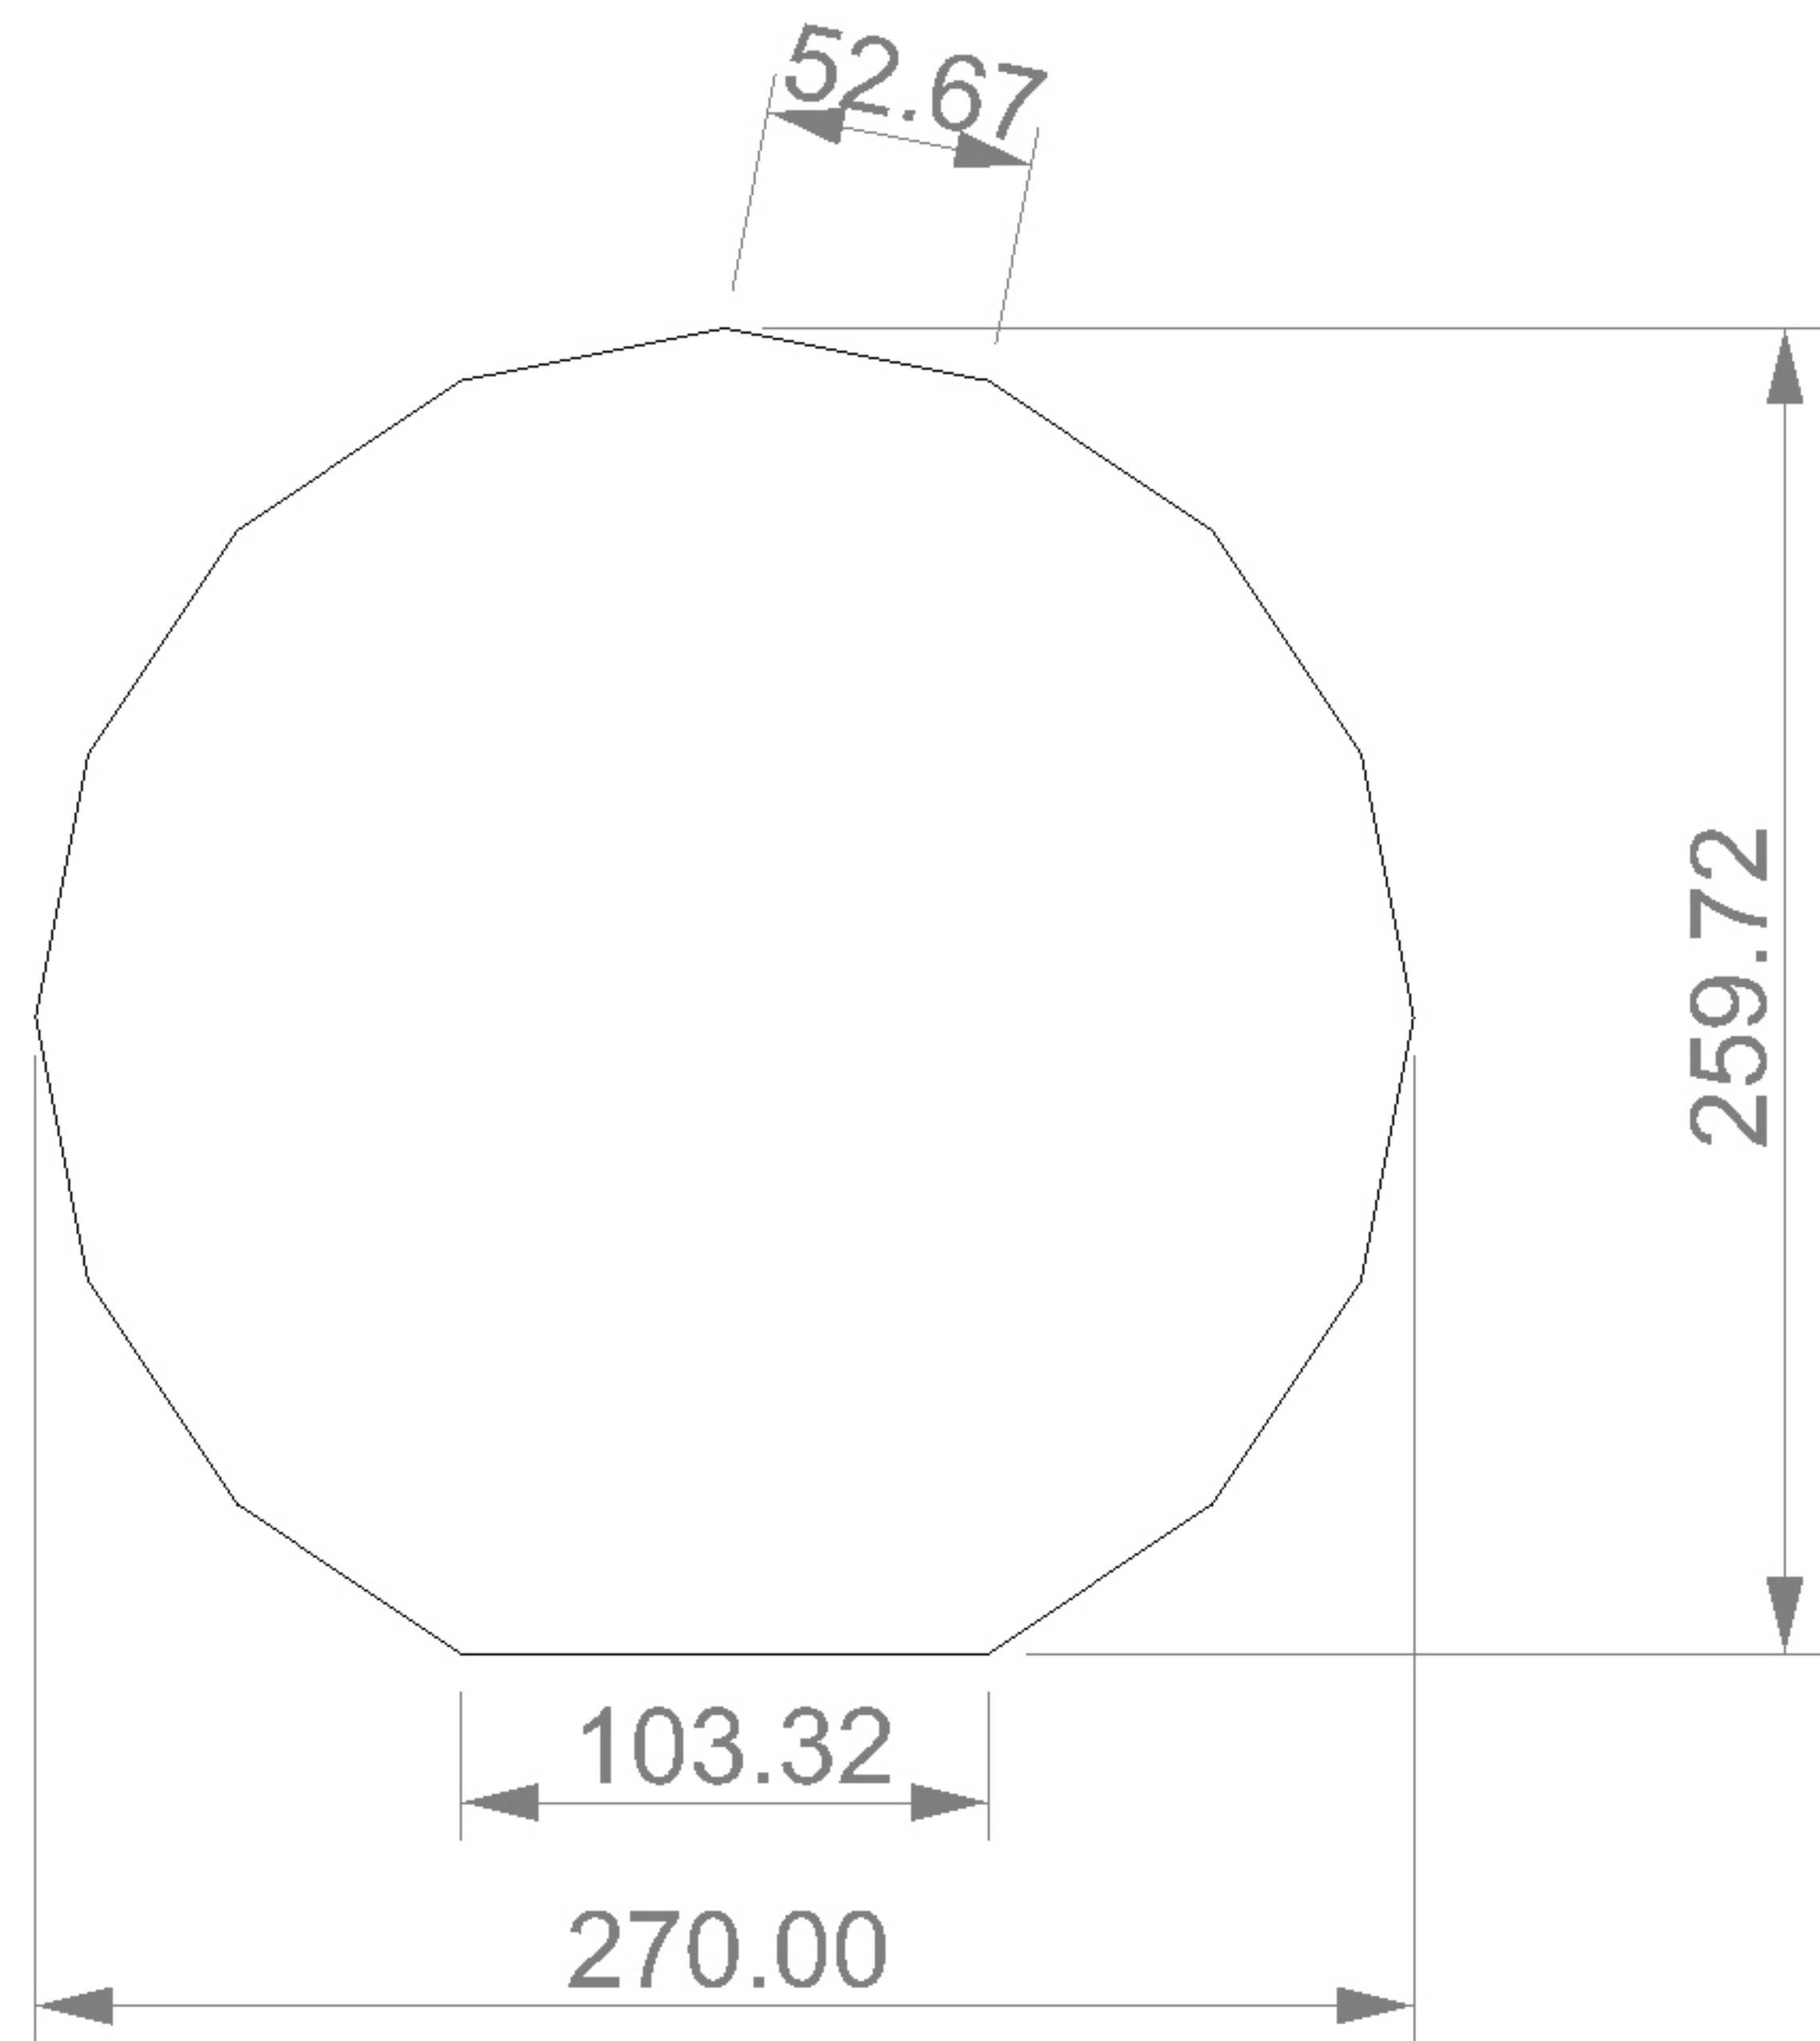


VISTA PERSPECTIVA

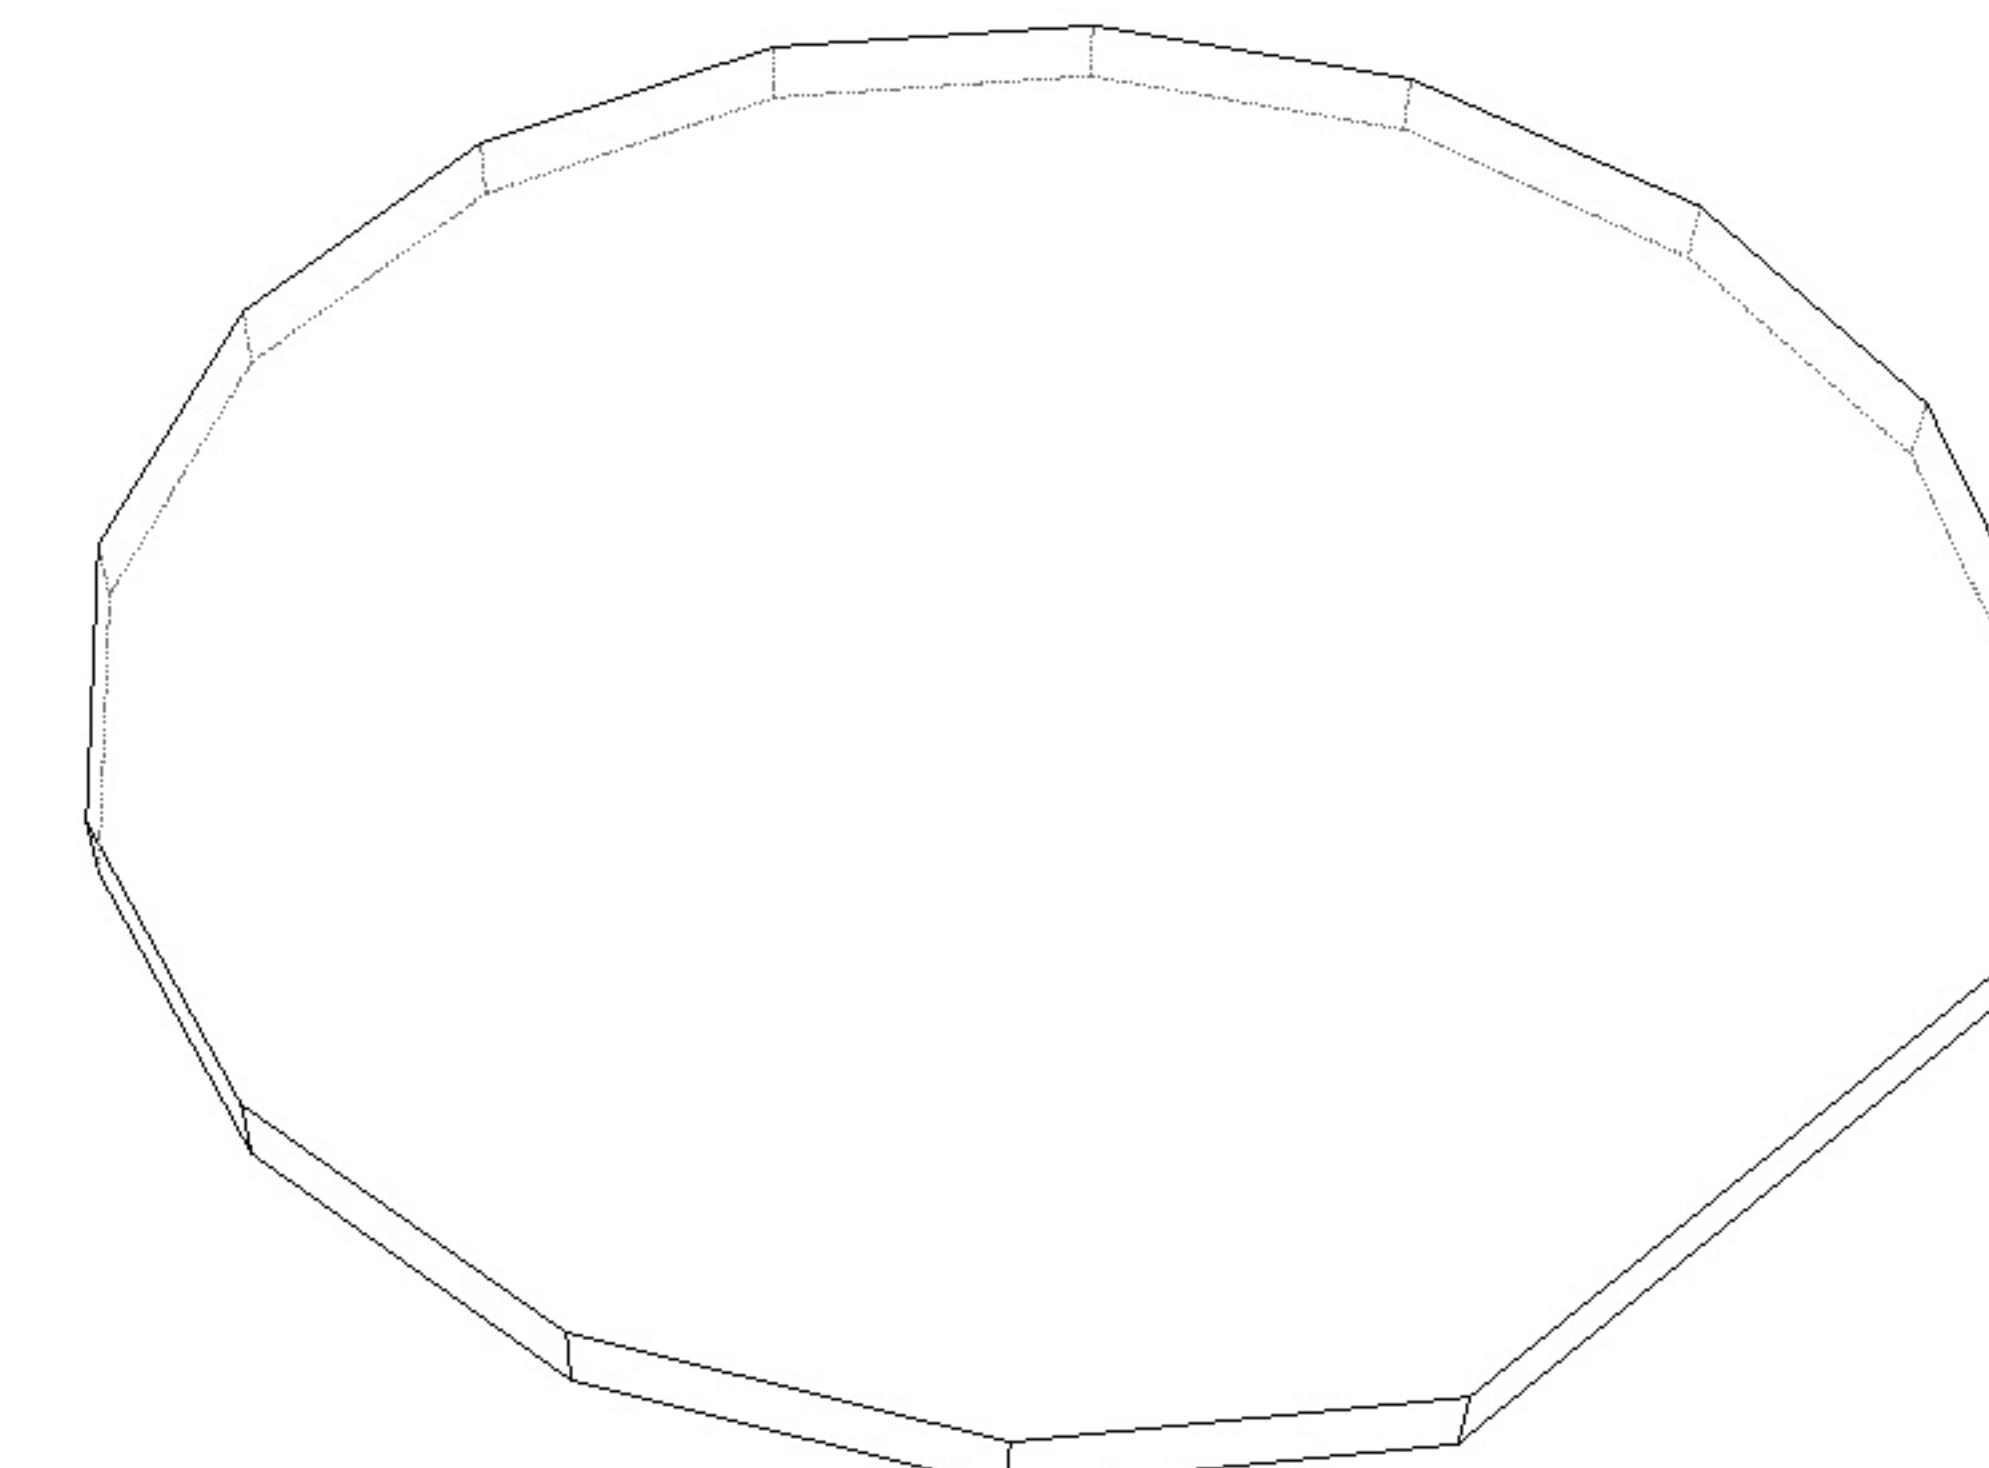

VISTA FRONTAL

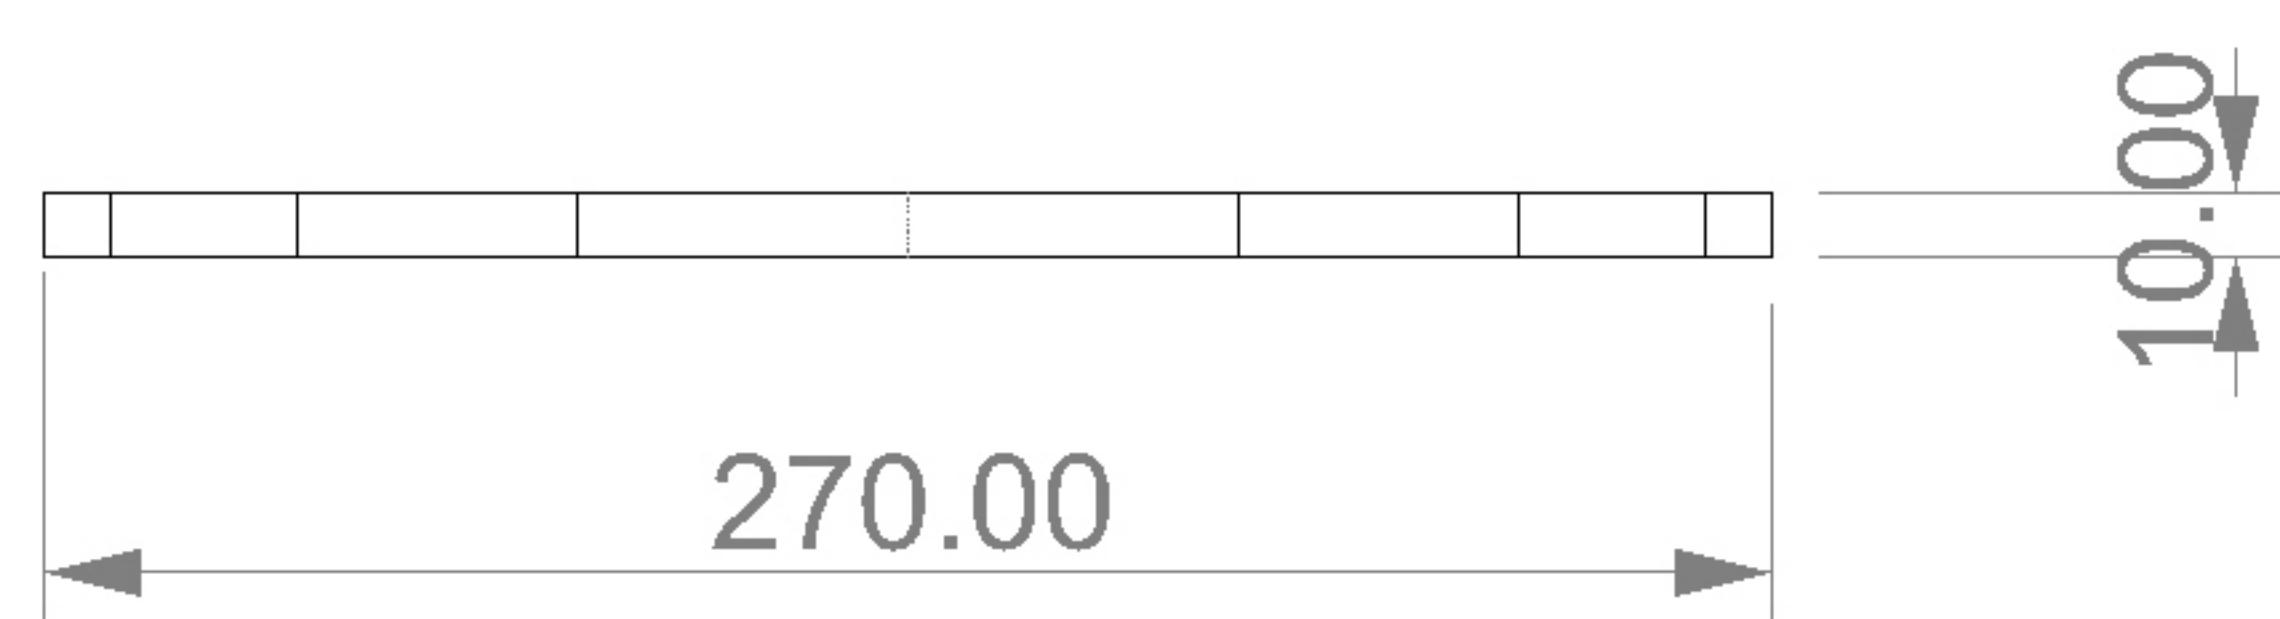

VISTA LATERAL

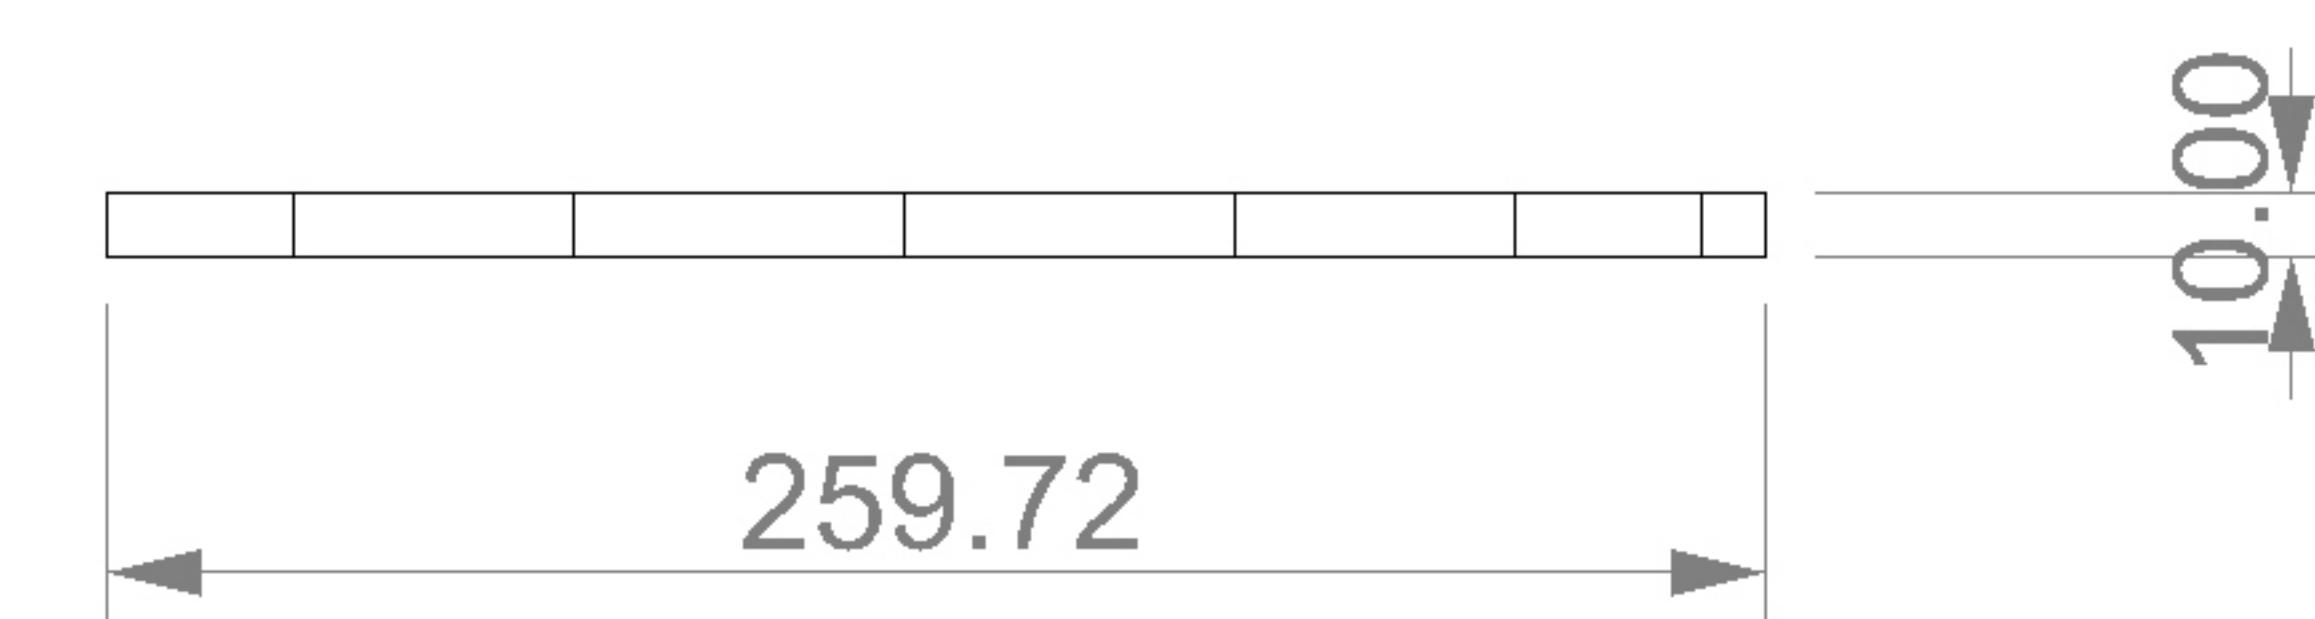

PROYECTO_Estructura caminar	DIMENSIONES GRALES: 270.00 x 10.00 x 259.72	ENSAMBLE GENERAL	11.MAYO.2020	
Estructura	OBSERVACIONES: MATERIALES: ESTRUCTURA DE MDF // TRIPLEY DE 16MM CON LAMINADO PLÁSTICO O ACABADOS SEGÚN CLIENTE		ACT. CM	
DIBUJÓ:fiscortes STUDIO			ESC. -	
			HOJA -	